


Municipal Road and Sewer Design

Plan and profile drawing package

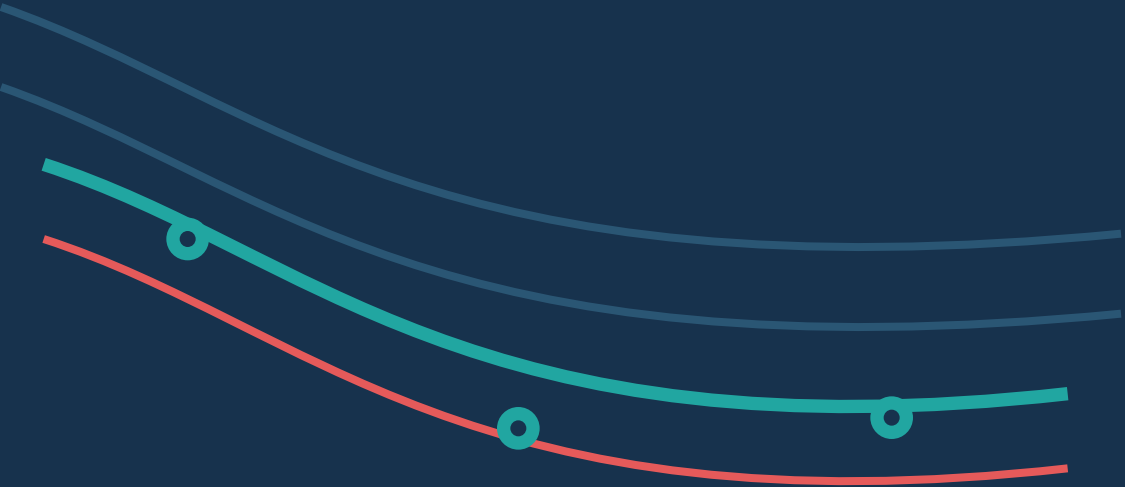

4

PLAN/PROFILE SHEETS

2

SEWER NETWORKS

1

ROAD CORRIDOR


PROJECT SCOPE


- Road corridor modelling and intersection coordination
- Storm and sanitary pipe networks with structures
- Plan/profile production, profile bands and sheet-set publishing
- Conceptual design based on publicly available mapping and terrain data

This independent conceptual exercise demonstrates development of a coordinated municipal road, storm sewer and sanitary sewer drawing package. The work focuses on Civil 3D modelling and drawing production rather than construction authorization or final engineering certification.

MODEL DEVELOPMENT	DRAWING PRODUCTION	COORDINATION CHECKS
- Existing-ground surface - Road alignment and profile - Corridor and intersection tie-ins - Storm and sanitary networks	- Plan and profile views - Pipe and structure annotation - Profile data bands - View frames, match lines and sheet set	- Network/profile consistency - Pipe slope and invert review - Structure placement - Plot readability and colour output

Data limitation: Existing conditions were interpreted from public GIS and LiDAR-derived terrain information. Utility locations, elevations, materials and capacities require survey, records review, field investigation and engineering verification before any real-world use.

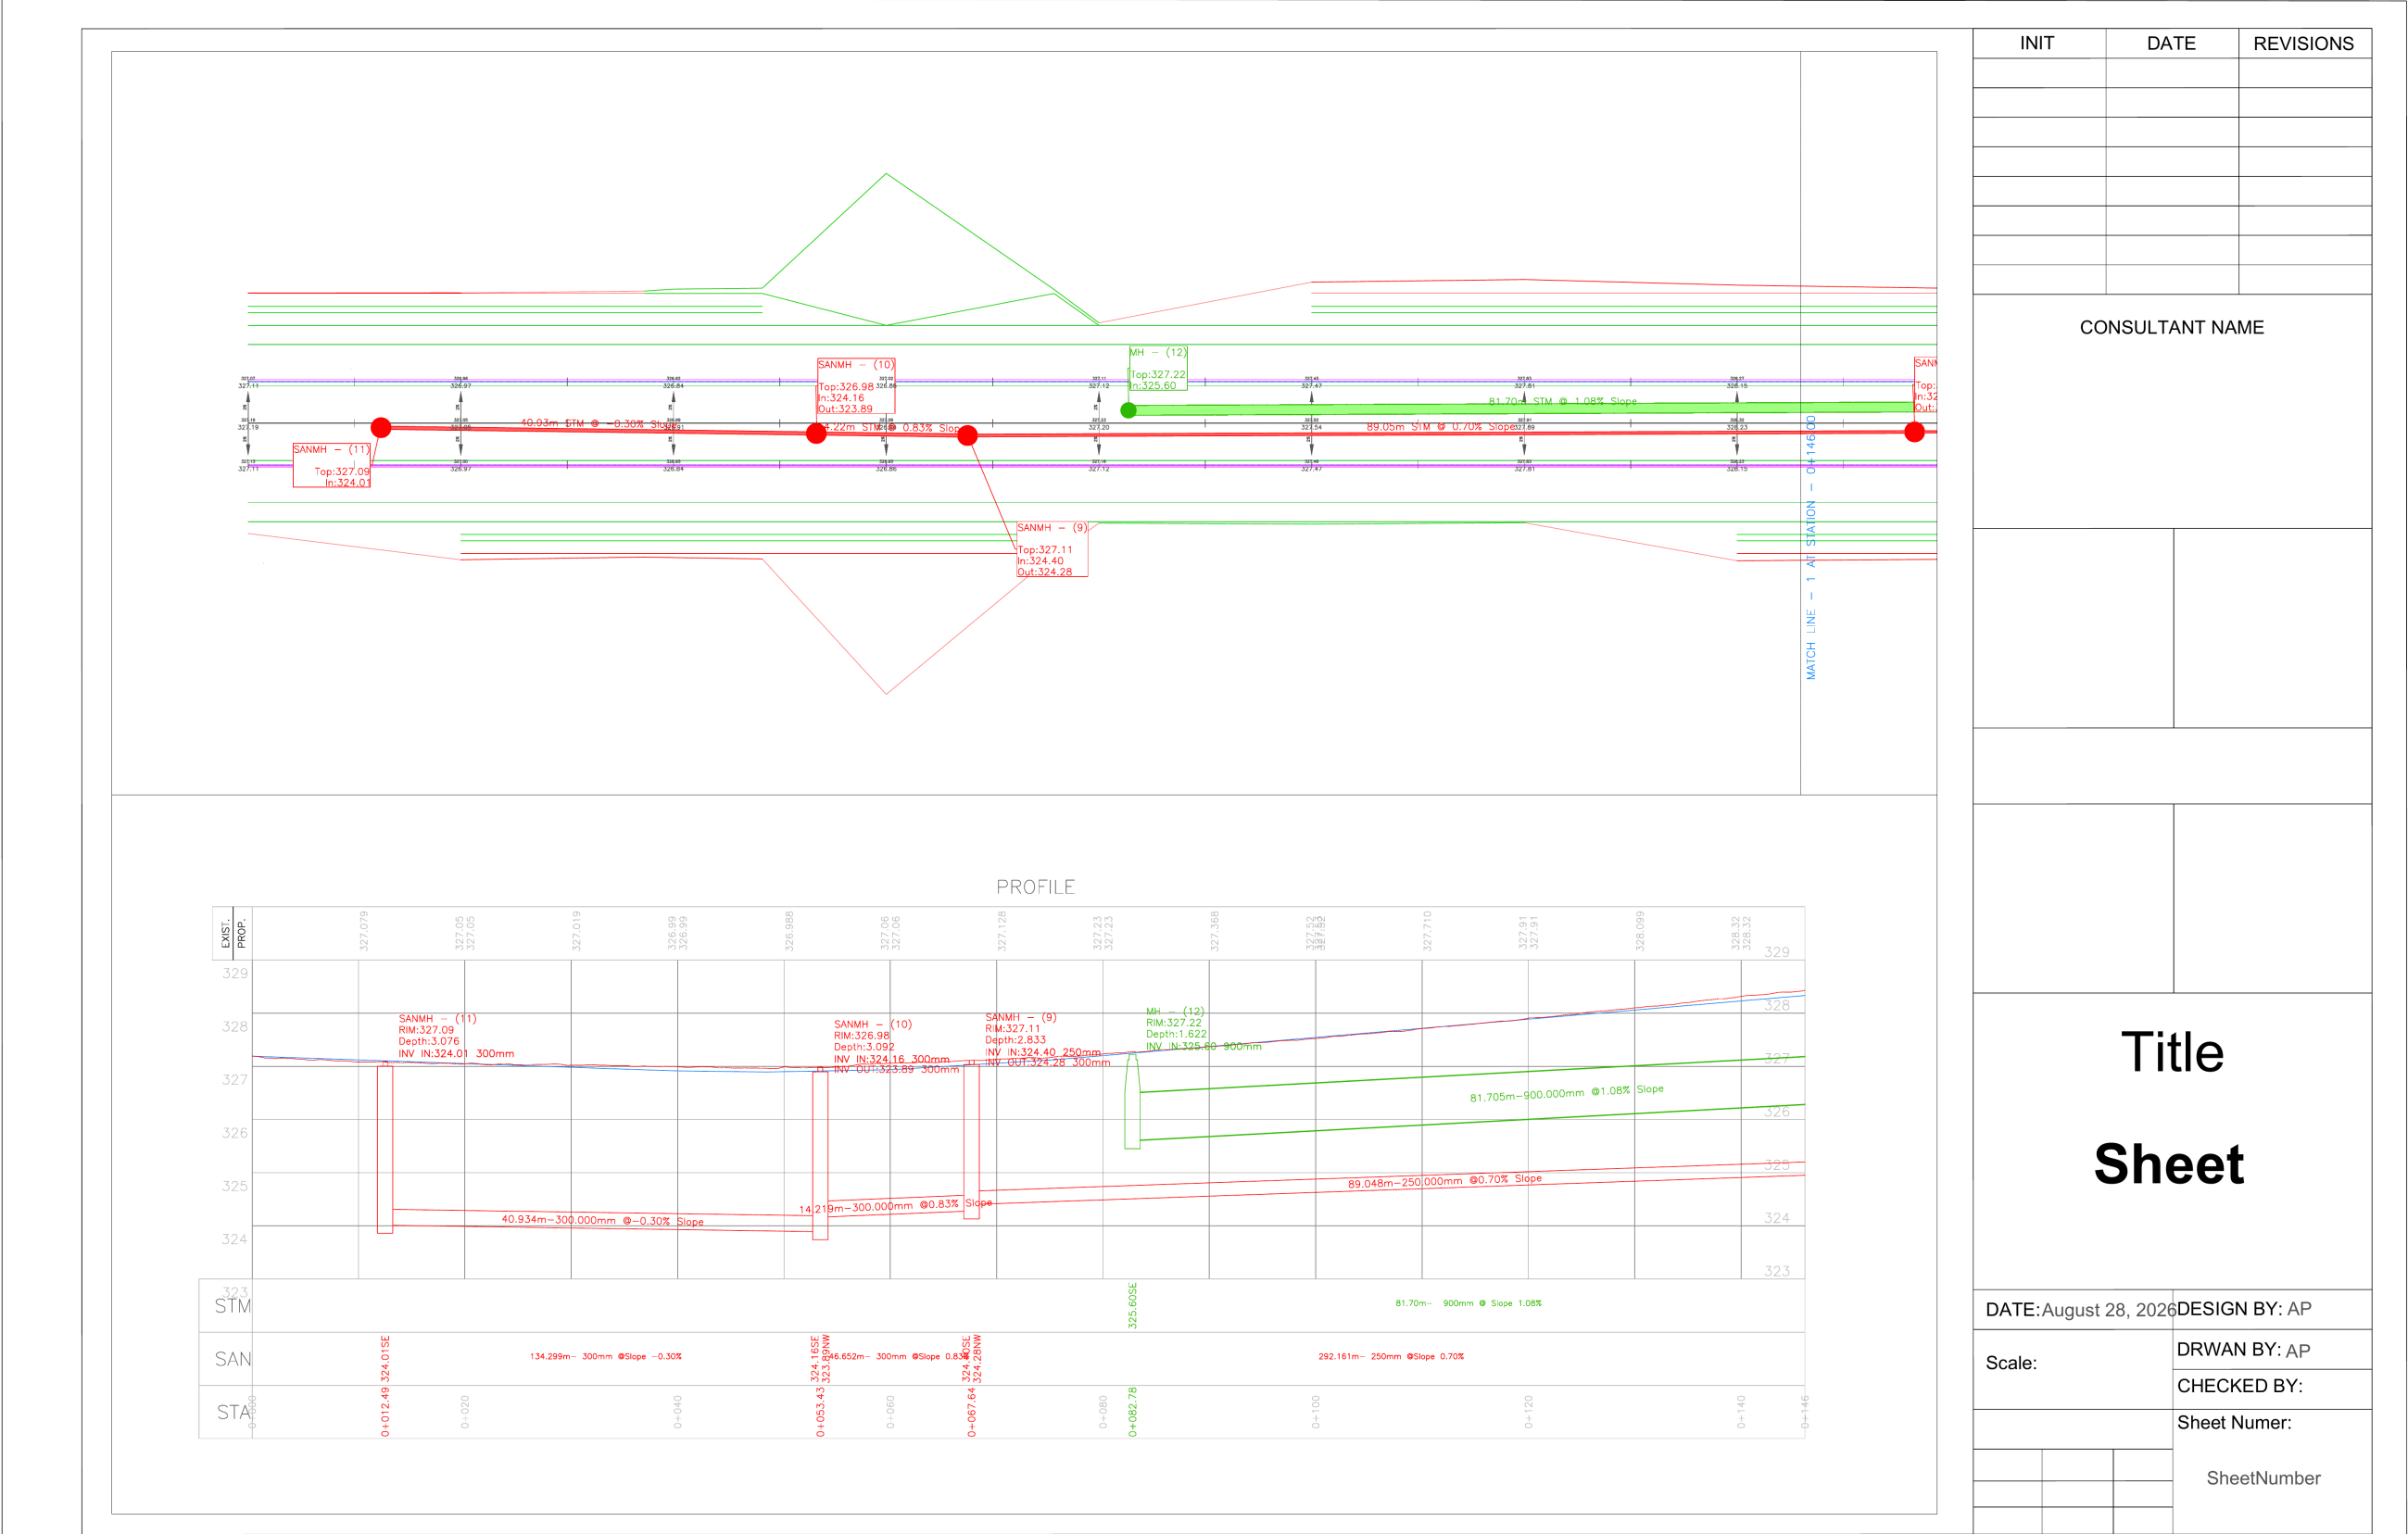



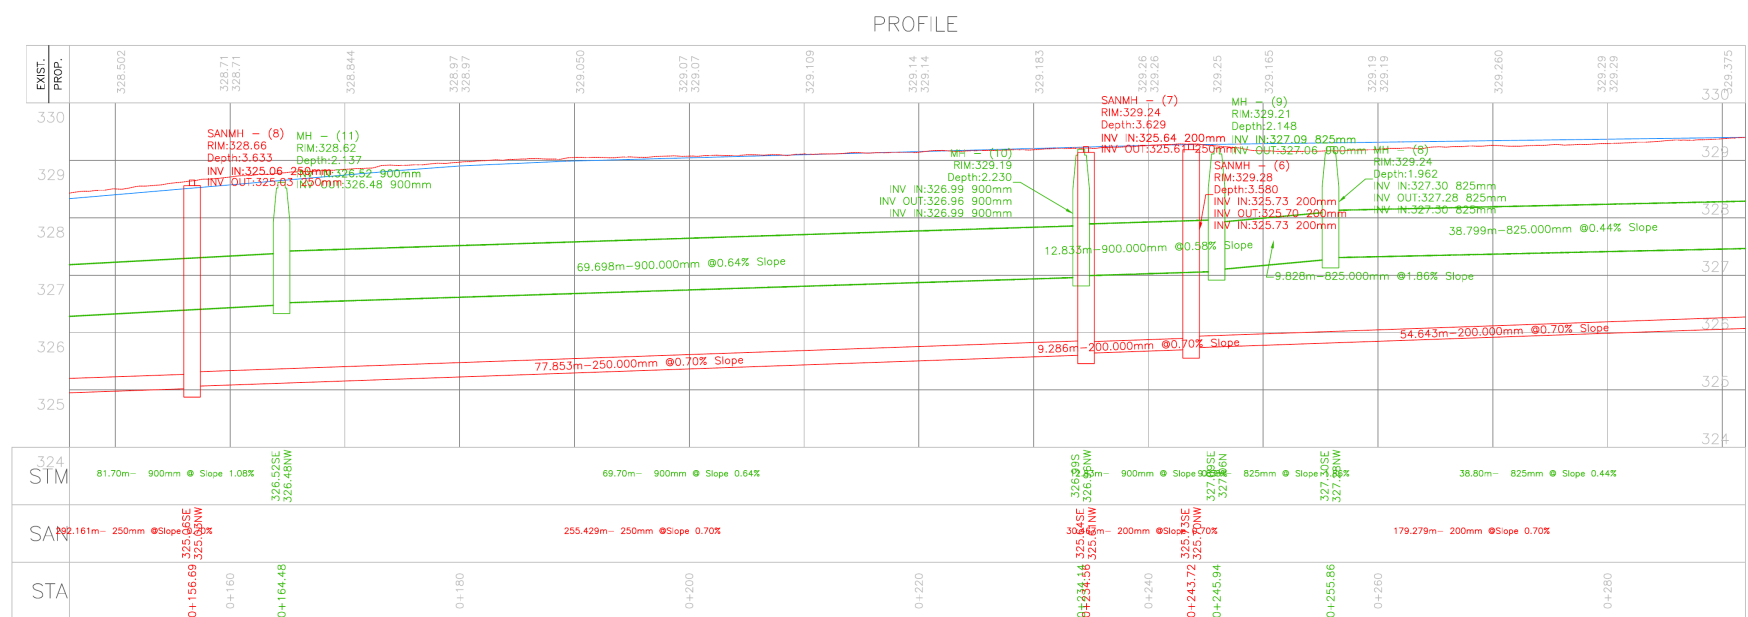


Title

Sheet

DATE: August 28, 2026			DESIGN BY: AP
Scale:			DRWAN BY: AP
			CHECKED BY:
			Sheet Numer:
			SheetNumber

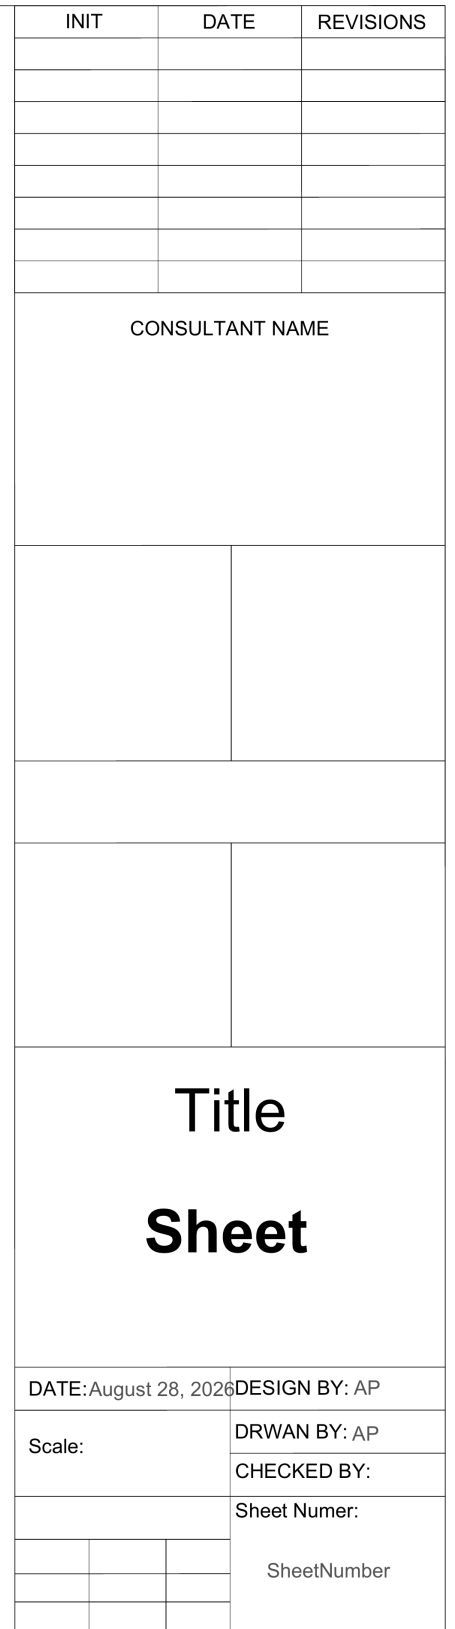

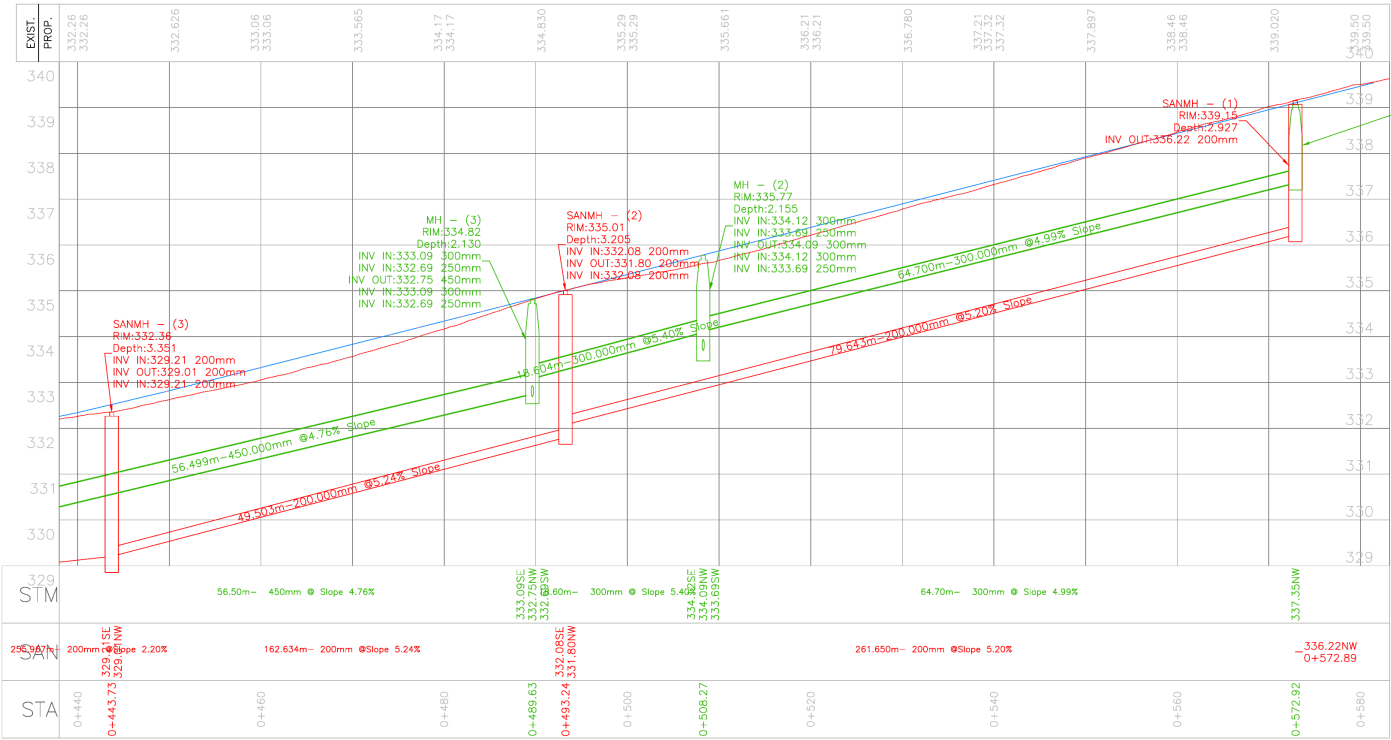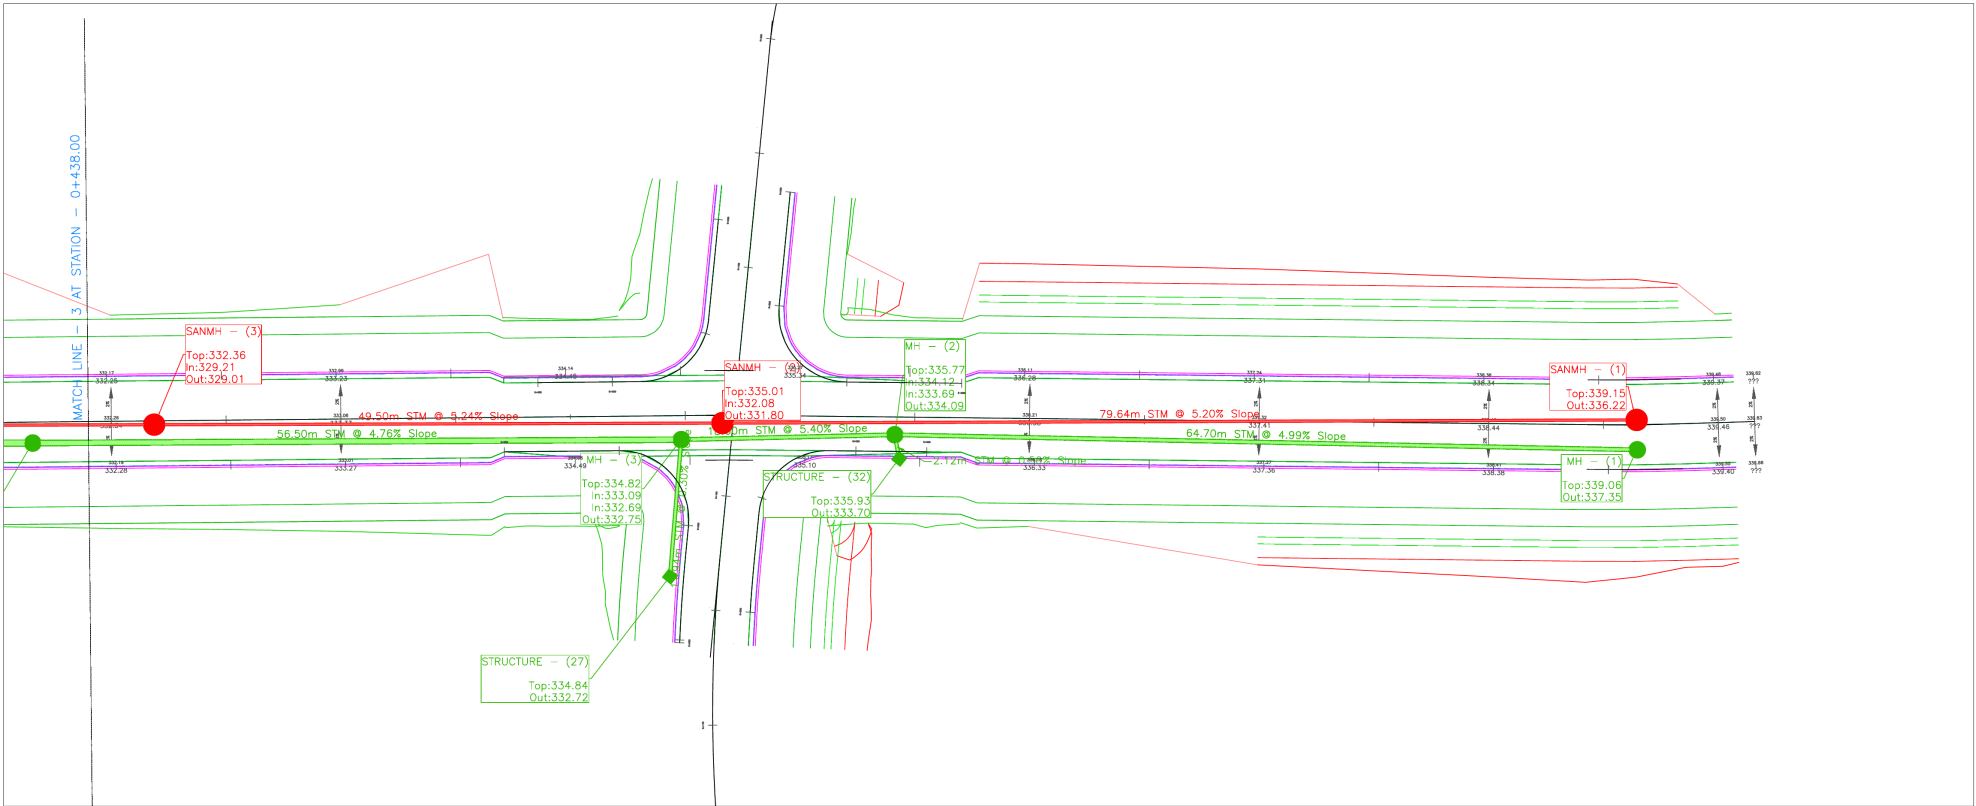

INIT	DATE	REVISIONS

CONSULTANT NAME

Title
Sheet

DATE: August 28, 2026	DESIGN BY: AP
Scale:	DRWAN BY: AP
	CHECKED BY:
	Sheet Numer:
	SheetNumber

Demonstrated Civil 3D capabilities

1

Surface and alignment

Organized an existing-ground model and used alignment-based plan/profile production.

2

Road corridor

Developed corridor geometry and coordinated lane-width transitions at intersections.

3

Pipe networks

Modelled storm and sanitary pipes, structures, profiles, styles and annotation.

4

Sheet production

Created view frames, match lines, profile views, data bands and a colour sheet-set publication.

PROFESSIONAL USE LIMITATION

The enclosed work is a skills demonstration. It is not an issued design, tender document, permit submission, record drawing or construction document, and it has not been independently reviewed or sealed.