


# Municipal Road and Sewer Design

Plan and profile drawing package

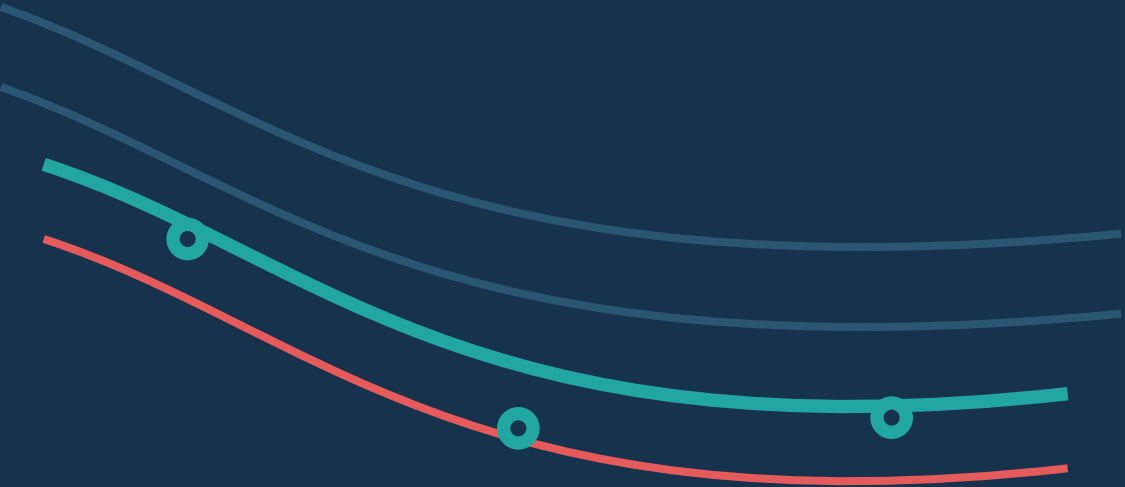

4

PLAN/PROFILE SHEETS

2

SEWER NETWORKS

1

ROAD CORRIDOR

## PROJECT SCOPE


- Road corridor modelling and intersection coordination
- Storm and sanitary pipe networks with structures
- Plan/profile production, profile bands and sheet-set publishing
- Conceptual design based on publicly available mapping and terrain data

# Design approach and responsibilities



This independent conceptual exercise demonstrates development of a coordinated municipal road, storm sewer and sanitary sewer drawing package. The work focuses on Civil 3D modelling and drawing production rather than construction authorization or final engineering certification.

| MODEL DEVELOPMENT   | DRAWING PRODUCTION   | COORDINATION CHECKS   |
|---|---|---|
| <ul style="list-style-type: none"><li>Existing-ground surface</li><li>Road alignment and profile</li><li>Corridor and intersection tie-ins</li><li>Storm and sanitary networks</li></ul> | <ul style="list-style-type: none"><li>Plan and profile views</li><li>Pipe and structure annotation</li><li>Profile data bands</li><li>View frames, match lines and sheet set</li></ul> | <ul style="list-style-type: none"><li>Network/profile consistency</li><li>Pipe slope and invert review</li><li>Structure placement</li><li>Plot readability and colour output</li></ul> |

Data limitation: Existing conditions were interpreted from public GIS and LiDAR-derived terrain information. Utility locations, elevations, materials and capacities require survey, records review, field investigation and engineering verification before any real-world use.

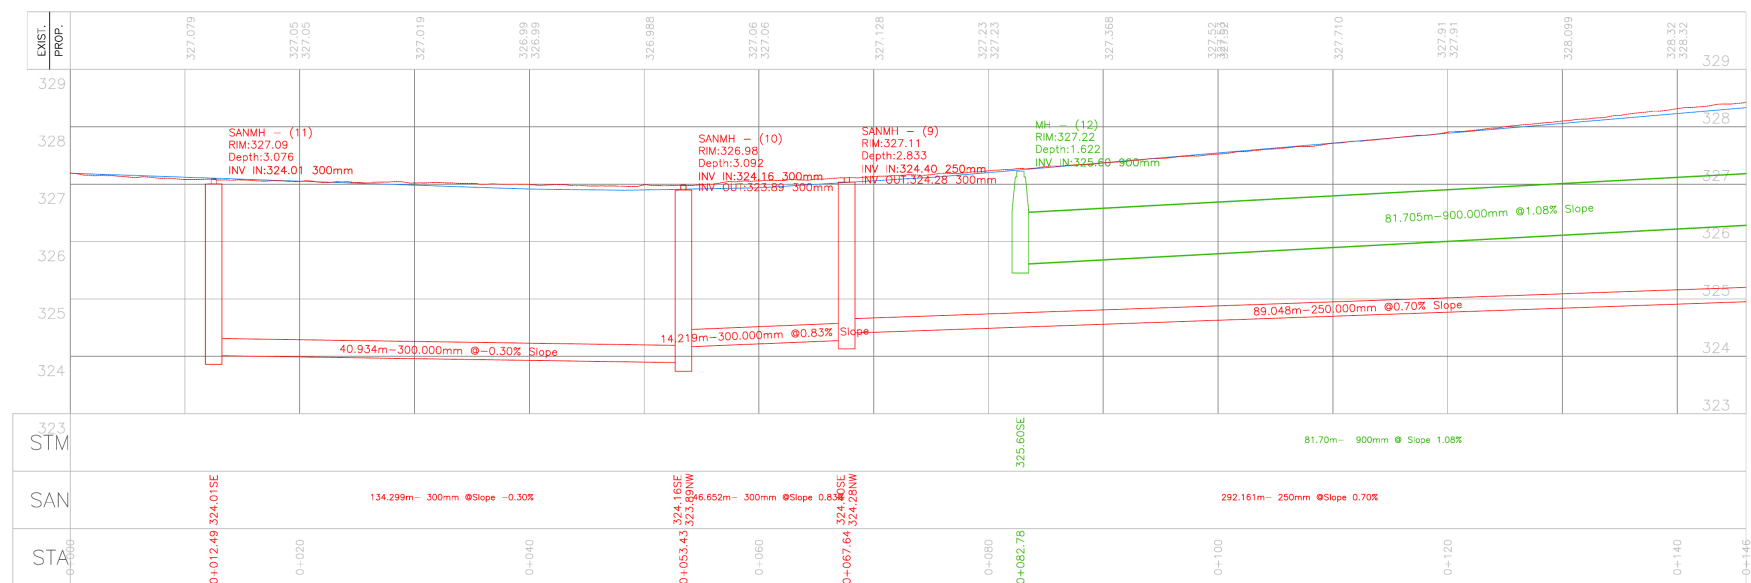

|                       |  |  |               |
|-----------------------|--|--|---------------|
| DATE: August 28, 2026 |  |  | DESIGN BY: AP |
| Scale:                |  |  | DRWAN BY: AP  |
|                       |  |  | CHECKED BY:   |
|                       |  |  | Sheet Number: |
|                       |  |  | SheetNumber   |
|                       |  |  |               |
|                       |  |  |               |

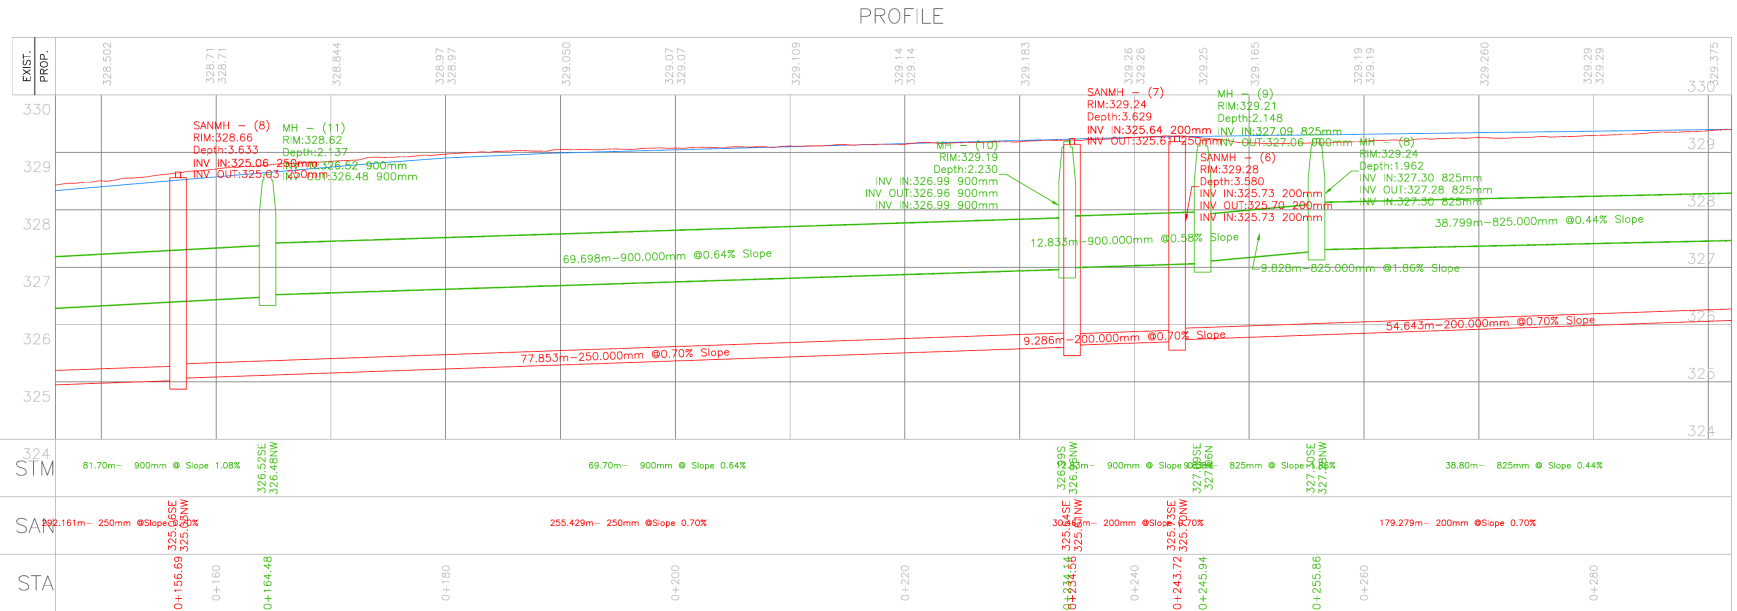
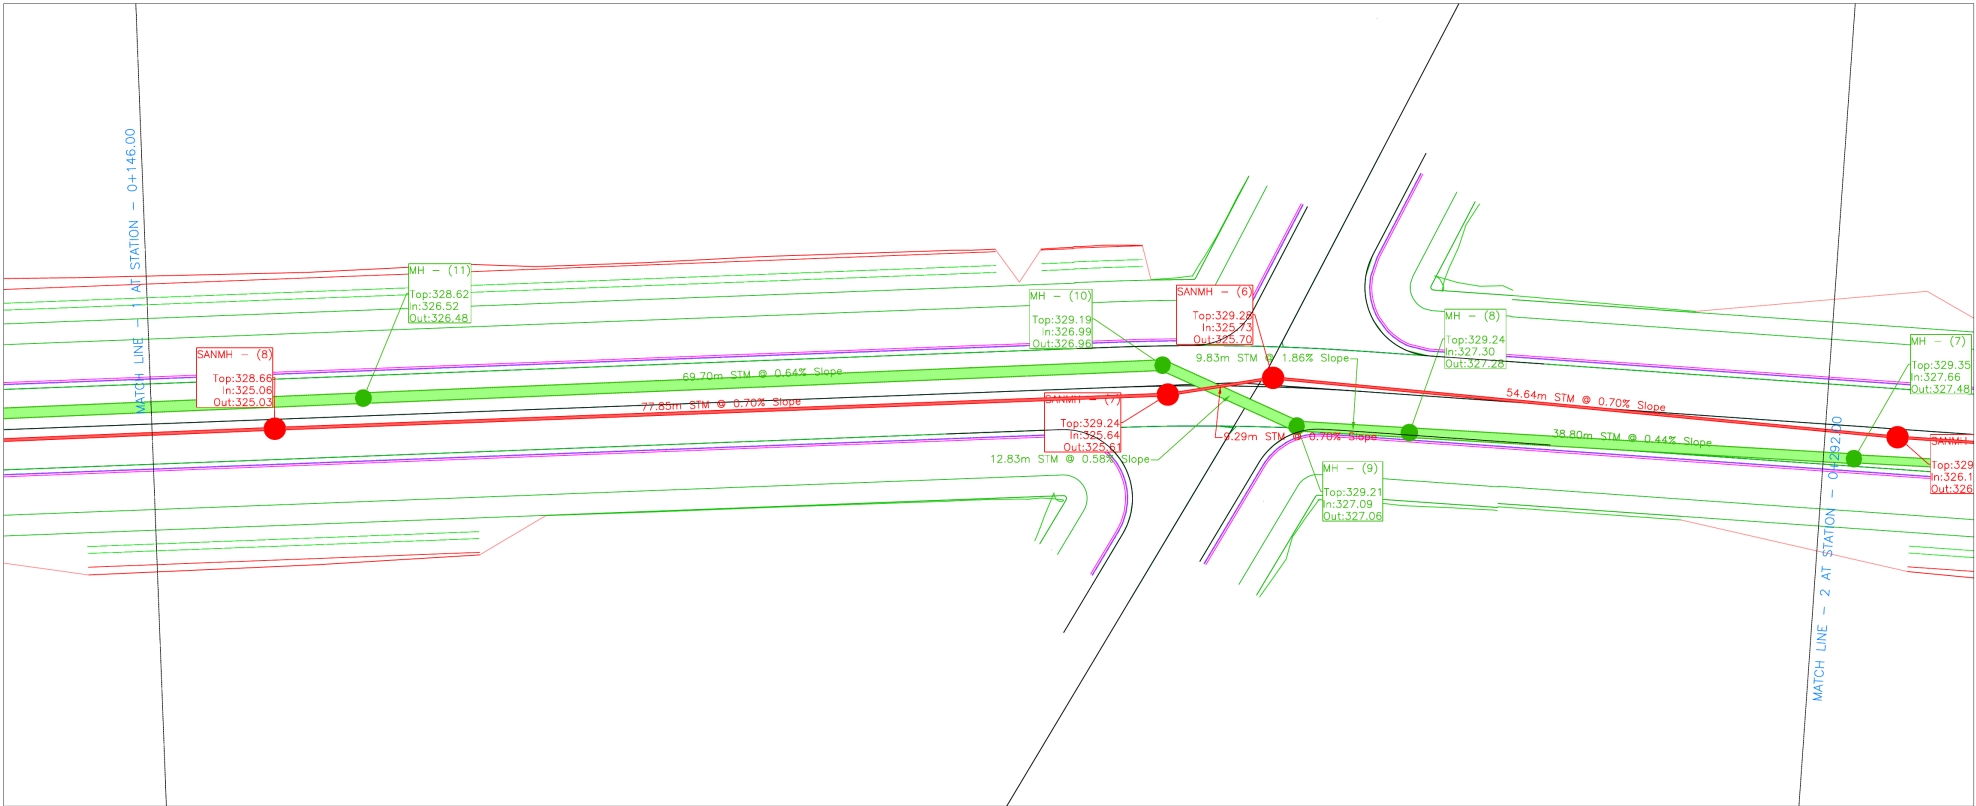


| INIT | DATE | REVISIONS |
|------|------|-----------|
|      |      |           |
|      |      |           |
CONSULTANT NAME

Title  
Sheet

|                       |               |
|-----------------------|---------------|
| DATE: August 28, 2026 | DESIGN BY: AP |
| Scale:                | DRWAN BY: AP  |
|                       | CHECKED BY:   |
|                       | Sheet Numer:  |
|                       | SheetNumber   |

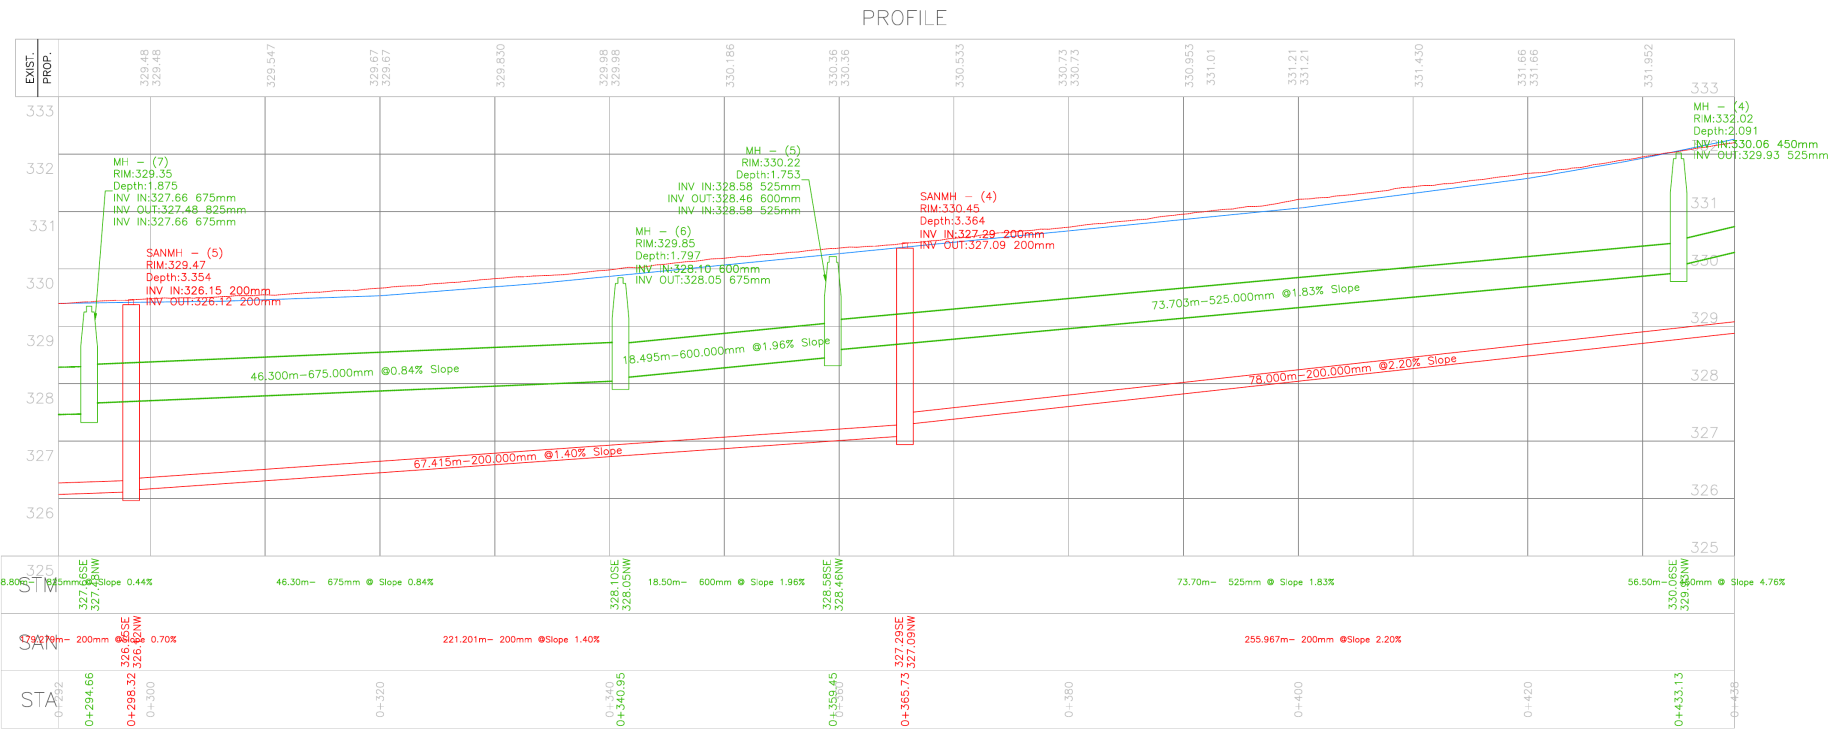
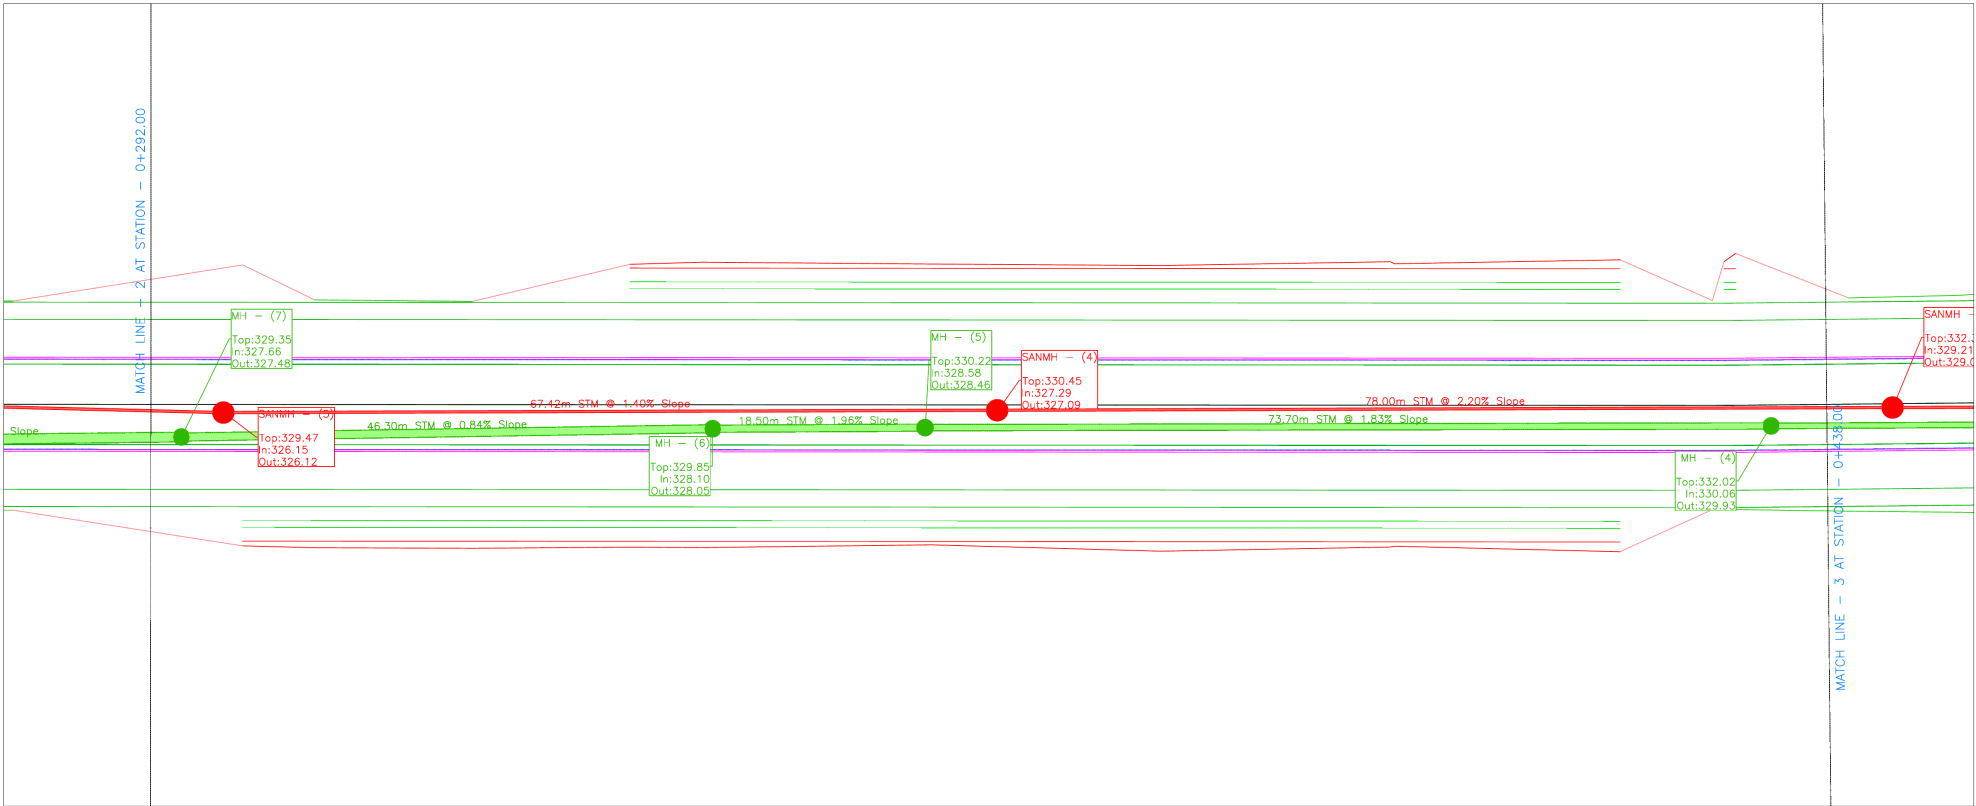


| INIT | DATE | REVISIONS |
|------|------|-----------|
|      |      |           |
|      |      |           |
CONSULTANT NAME

Title Sheet

|                       |               |
|-----------------------|---------------|
| DATE: August 28, 2026 | DESIGN BY: AP |
| Scale:                | DRWAN BY: AP  |
|                       | CHECKED BY:   |
|                       | Sheet Numer:  |
|                       | SheetNumber   |

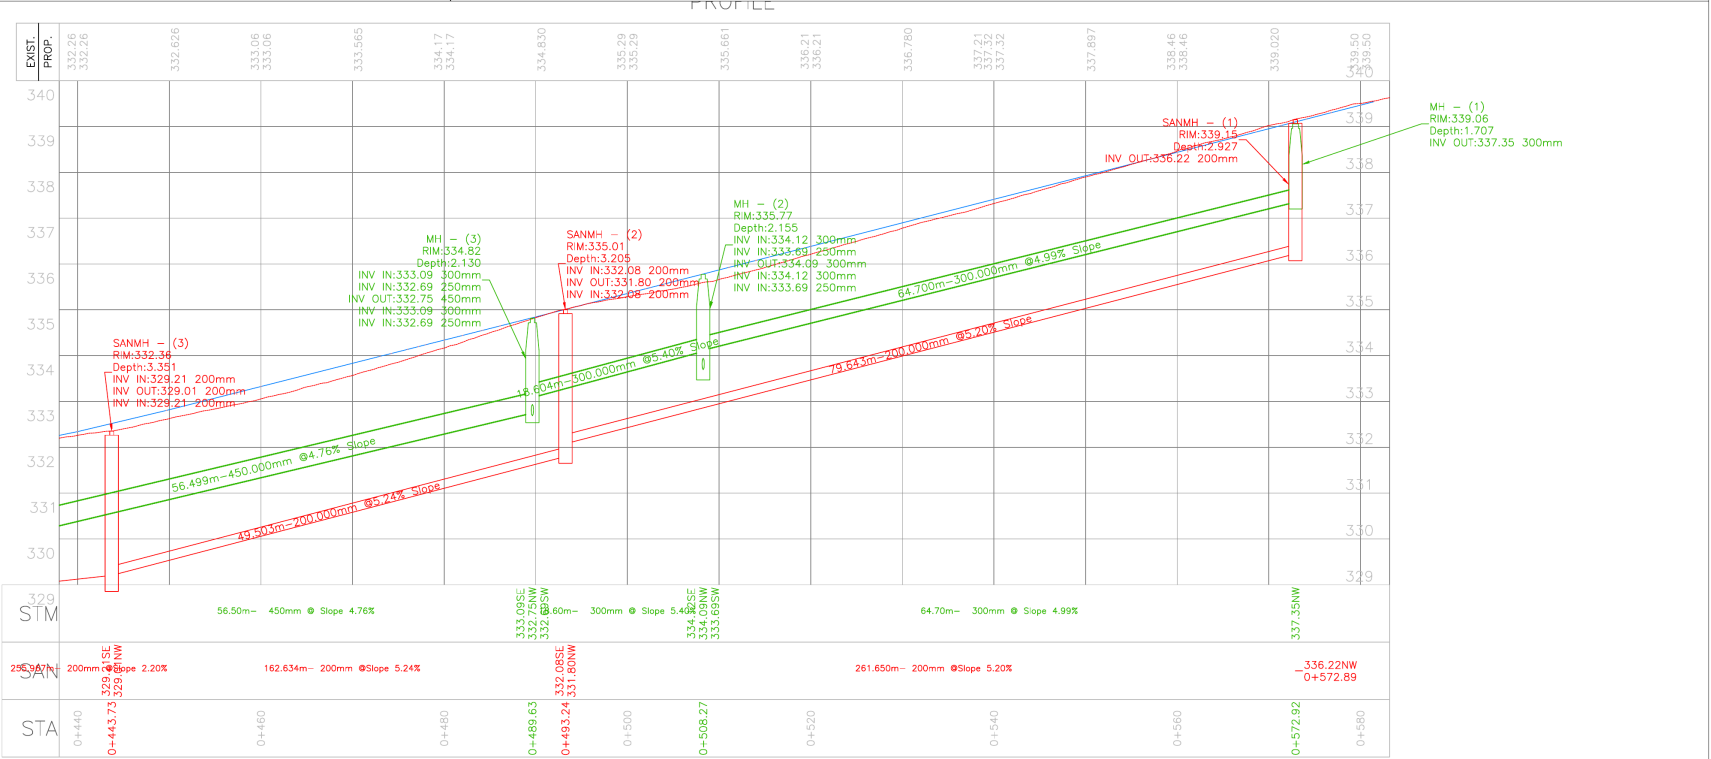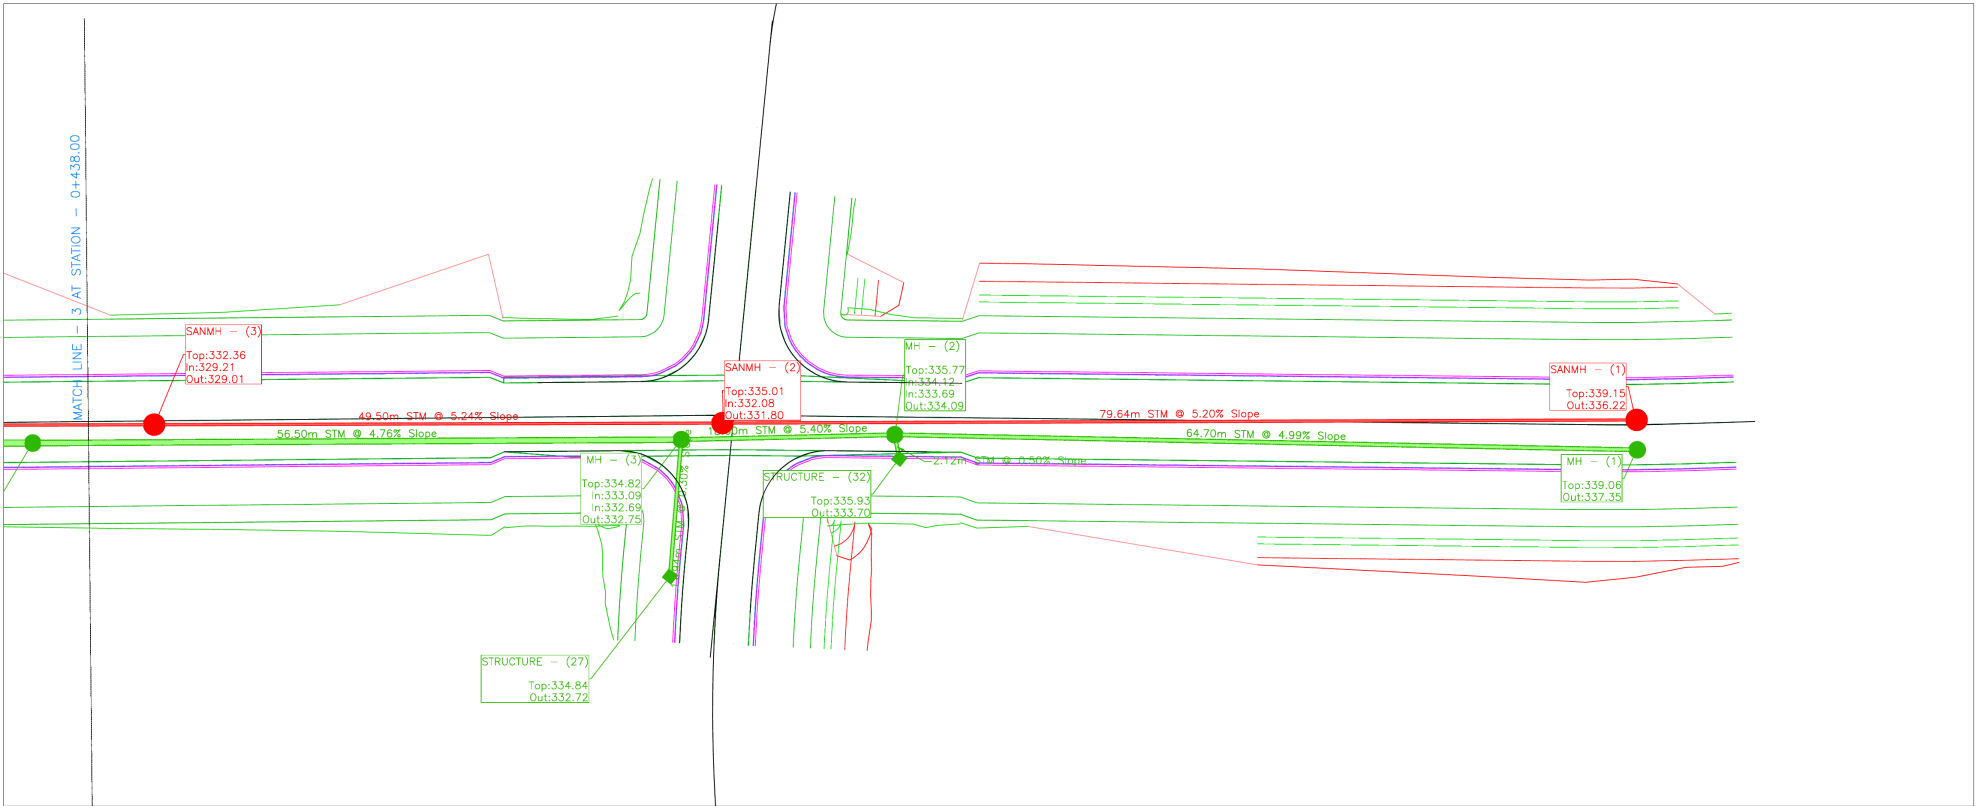

| INIT | DATE | REVISIONS |
|------|------|-----------|
|      |      |           |
|      |      |           |
CONSULTANT NAME

Title  
Sheet

|                       |               |
|-----------------------|---------------|
| DATE: August 28, 2026 | DESIGN BY: AP |
| Scale:                | DRWAN BY: AP  |
|                       | CHECKED BY:   |
|                       | Sheet Numer:  |
|                       | SheetNumber   |



# Demonstrated Civil 3D capabilities

1

## Surface and alignment

Organized an existing-ground model and used alignment-based plan/profile production.

2

## Road corridor

Developed corridor geometry and coordinated lane-width transitions at intersections.

3

## Pipe networks

Modelled storm and sanitary pipes, structures, profiles, styles and annotation.

4

## Sheet production

Created view frames, match lines, profile views, data bands and a colour sheet-set publication.

### PROFESSIONAL USE LIMITATION

The enclosed work is a skills demonstration. It is not an issued design, tender document, permit submission, record drawing or construction document, and it has not been independently reviewed or sealed.