


Municipal Road and Sewer Design

Conceptual plan and profile drawing package

CORE CAPABILITIES

- Road corridor and intersection coordination
- Storm and sanitary plan/profile production
- Conceptual GIS/LiDAR-based existing-condition modelling

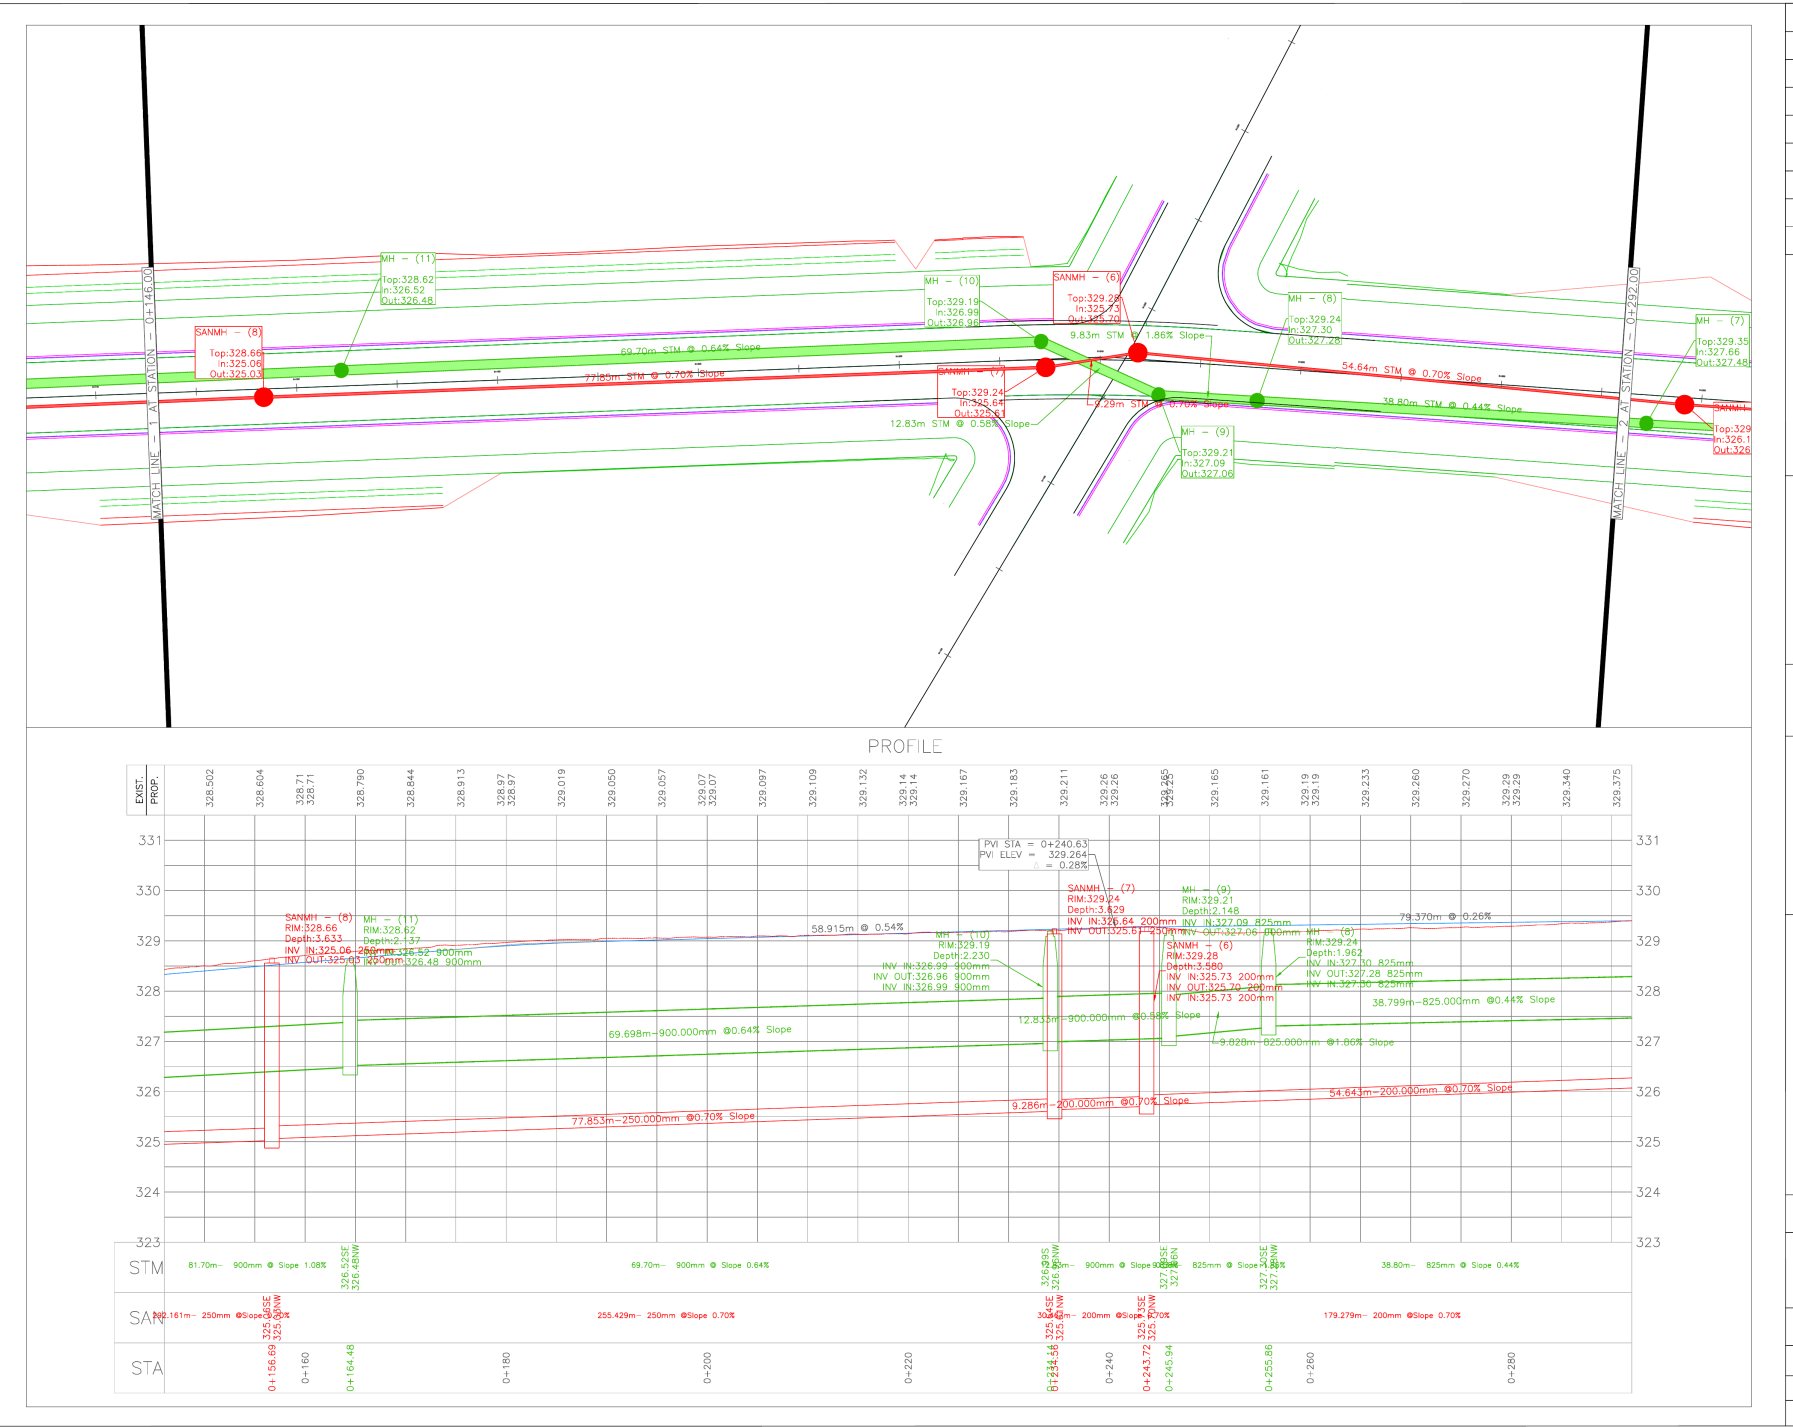

Design approach and responsibilities

This independent conceptual exercise demonstrates a coordinated municipal road, storm sewer and sanitary sewer drawing package. The focus is Civil 3D modelling, plan/profile coordination and drawing production—not construction authorization or final engineering certification.

MODEL DEVELOPMENT


- Existing-ground surface
- Road alignment and profile
- Corridor and intersection tie-ins
- Storm and sanitary networks



DRAWING PRODUCTION

- Plan and profile views
- Pipe and structure annotation
- Profile data bands
- View frames and match lines

QUALITY REVIEW

- Network/profile consistency
- Pipe slopes and inverts
- Structure placement
- Colour plot readability

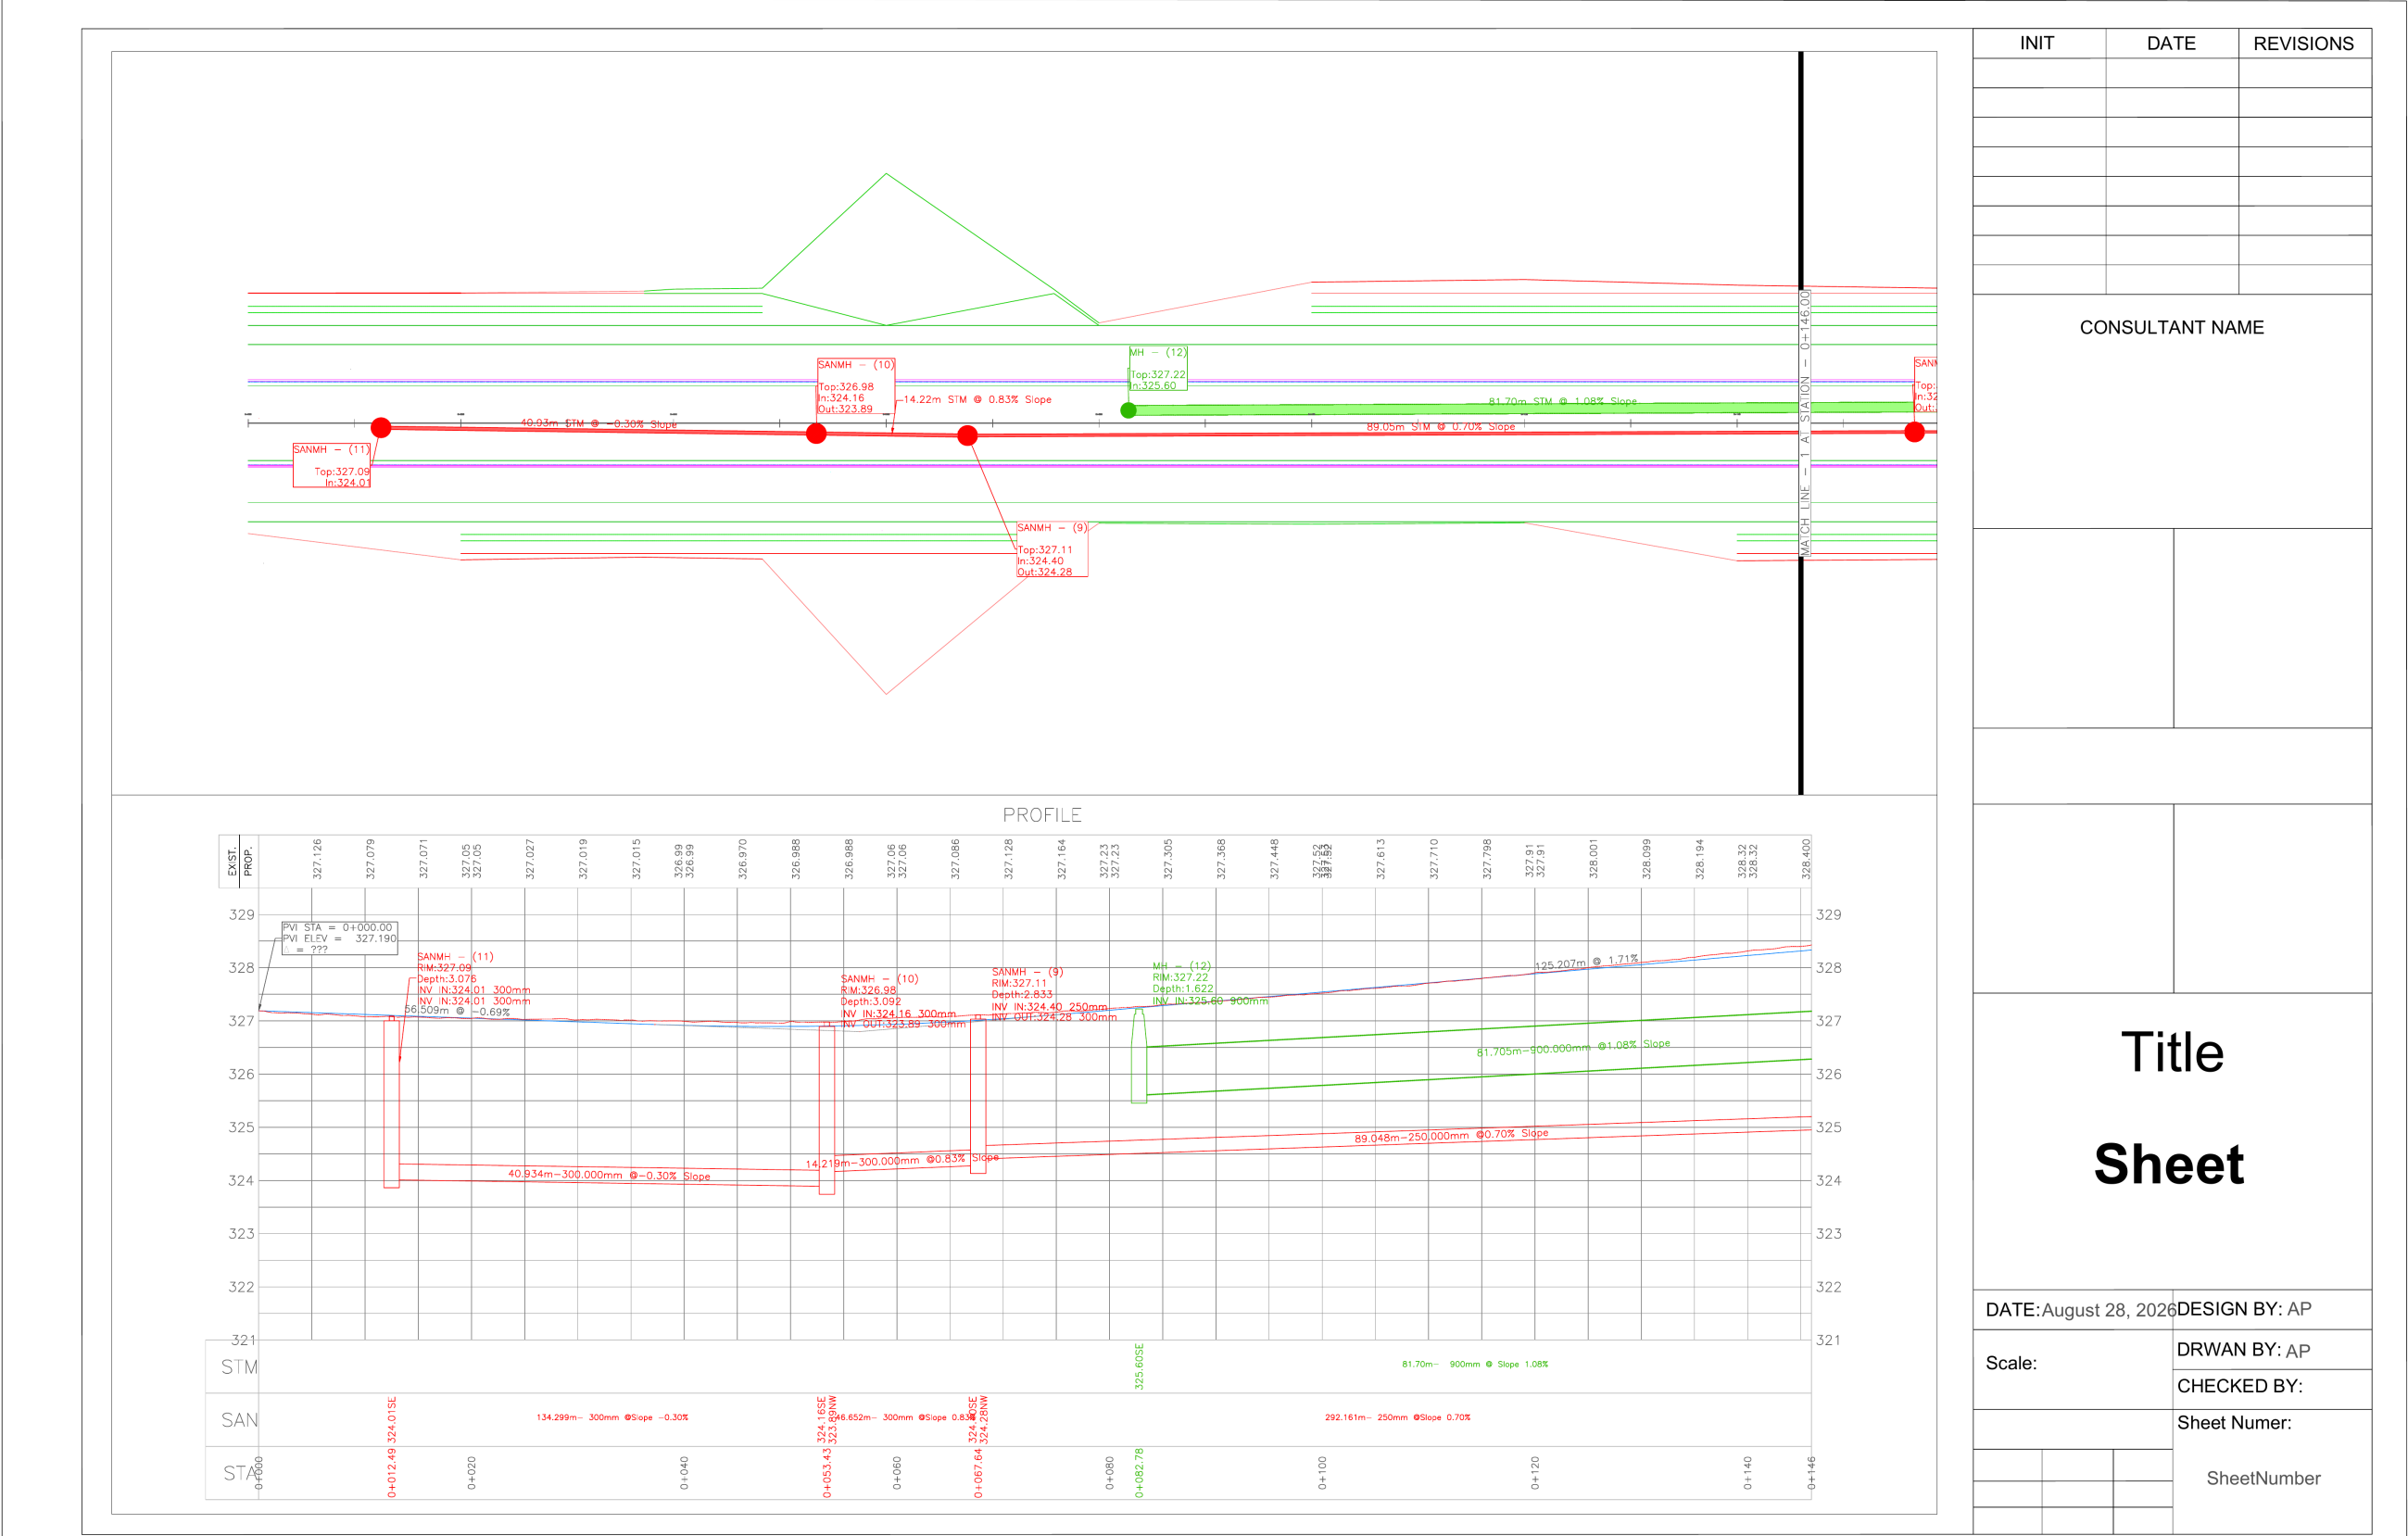

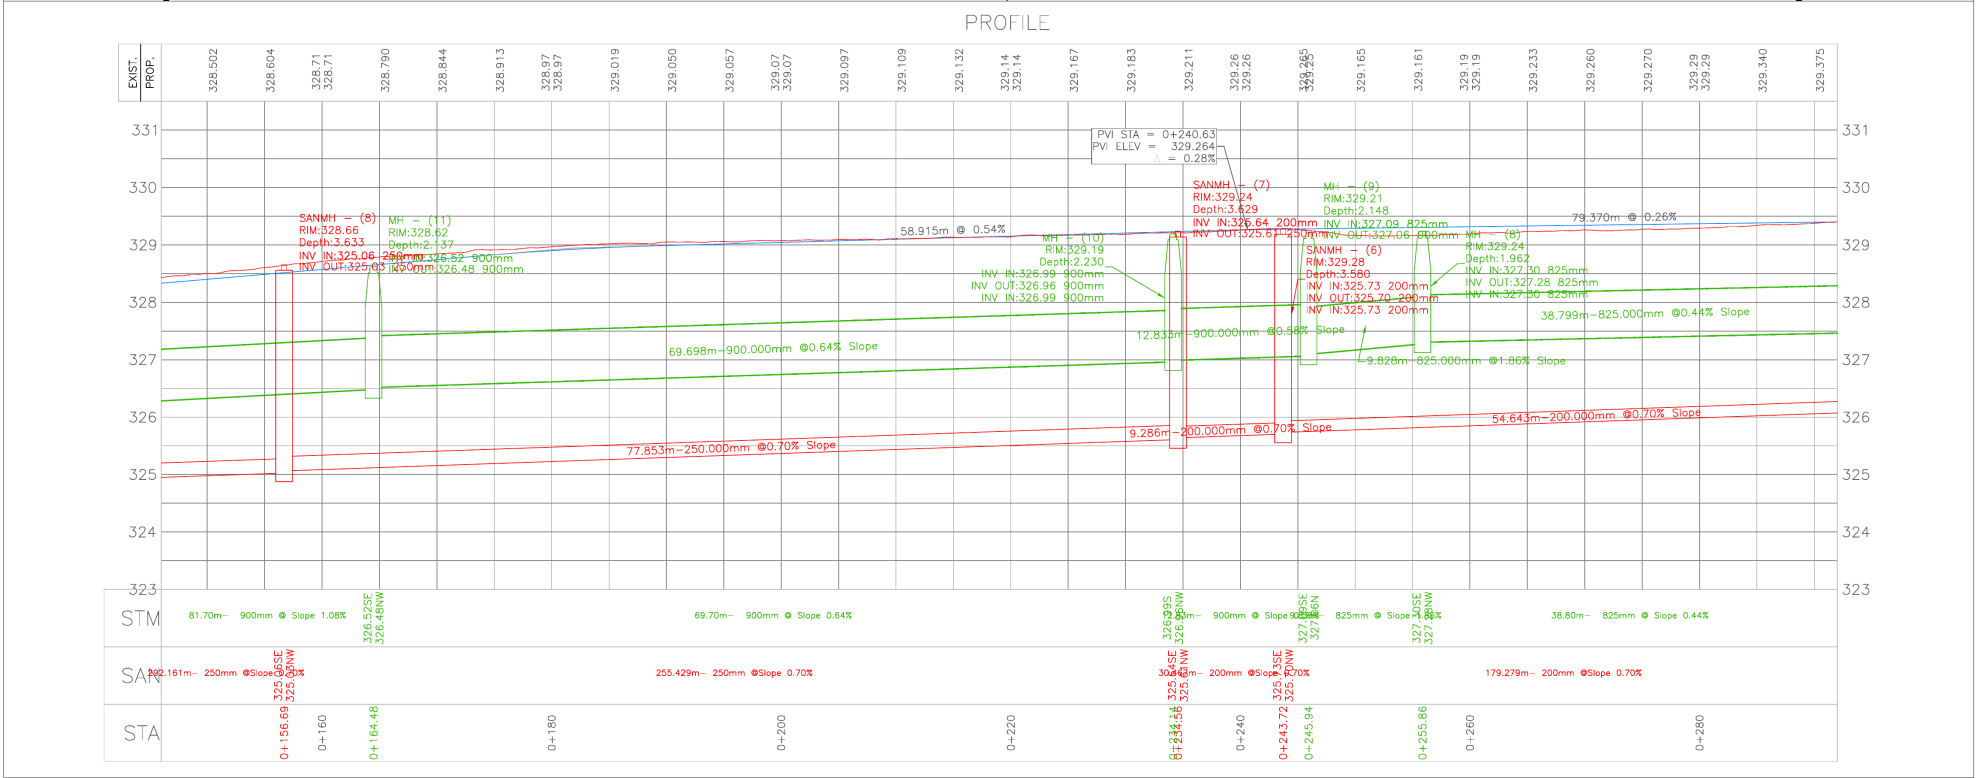
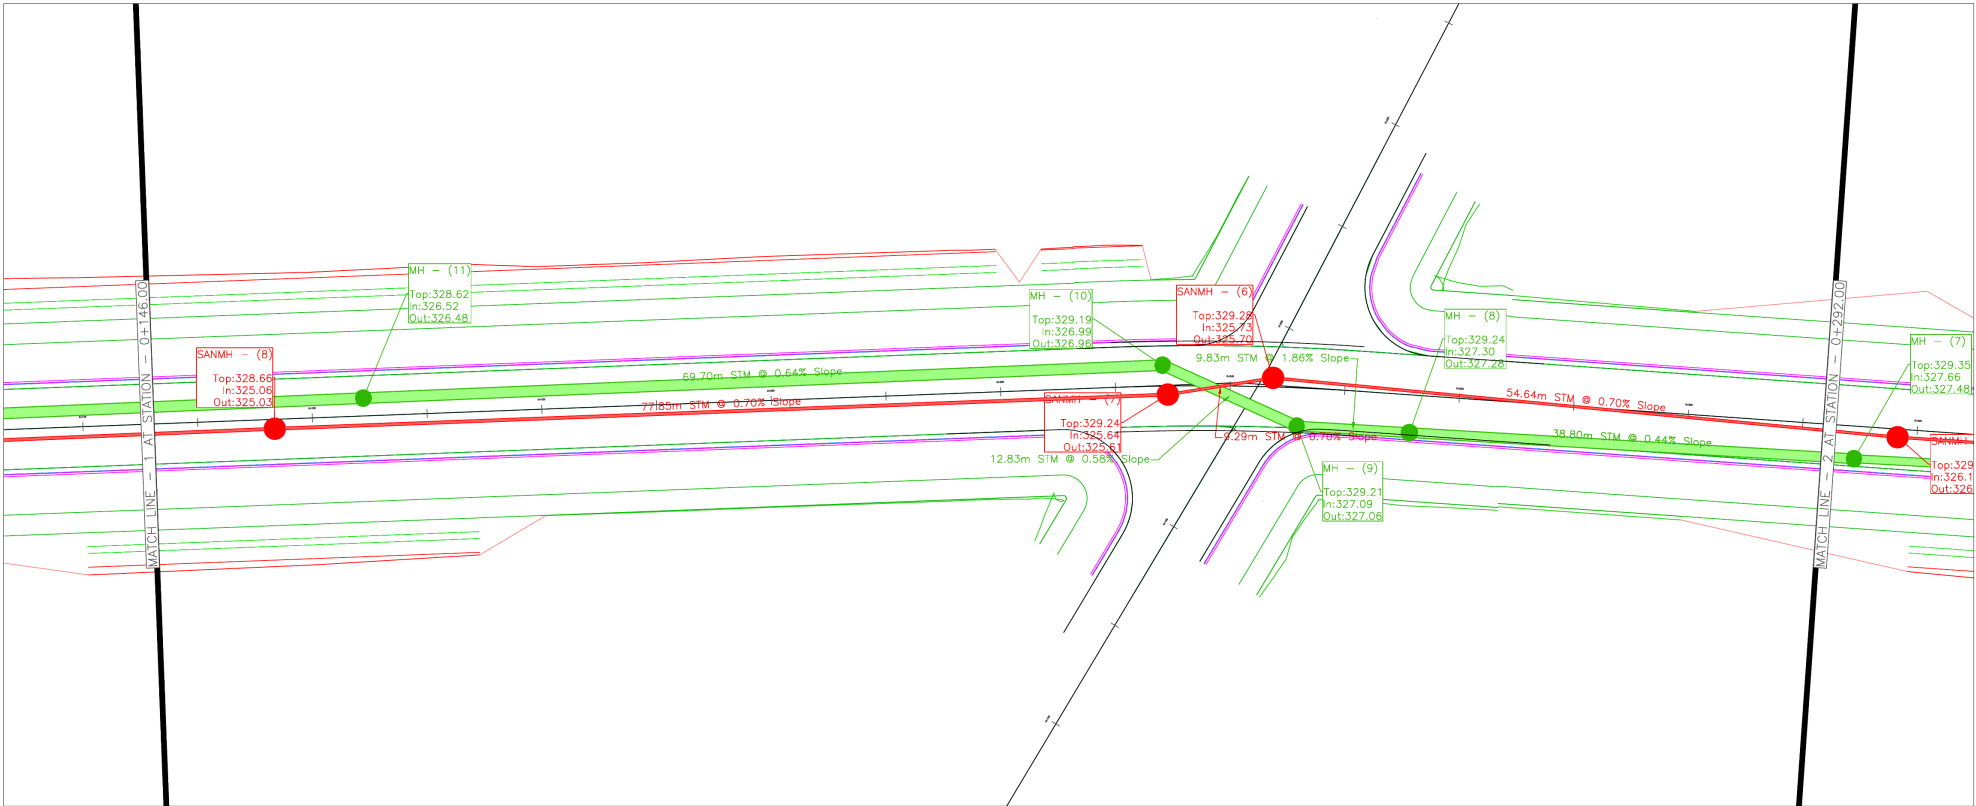


INIT	DATE	REVISIONS

CONSULTANT NAME

Title
Sheet

DATE: August 28, 2026	DESIGN BY: AP
Scale:	DRWAN BY: AP
	CHECKED BY:
	Sheet Numer:
	SheetNumber

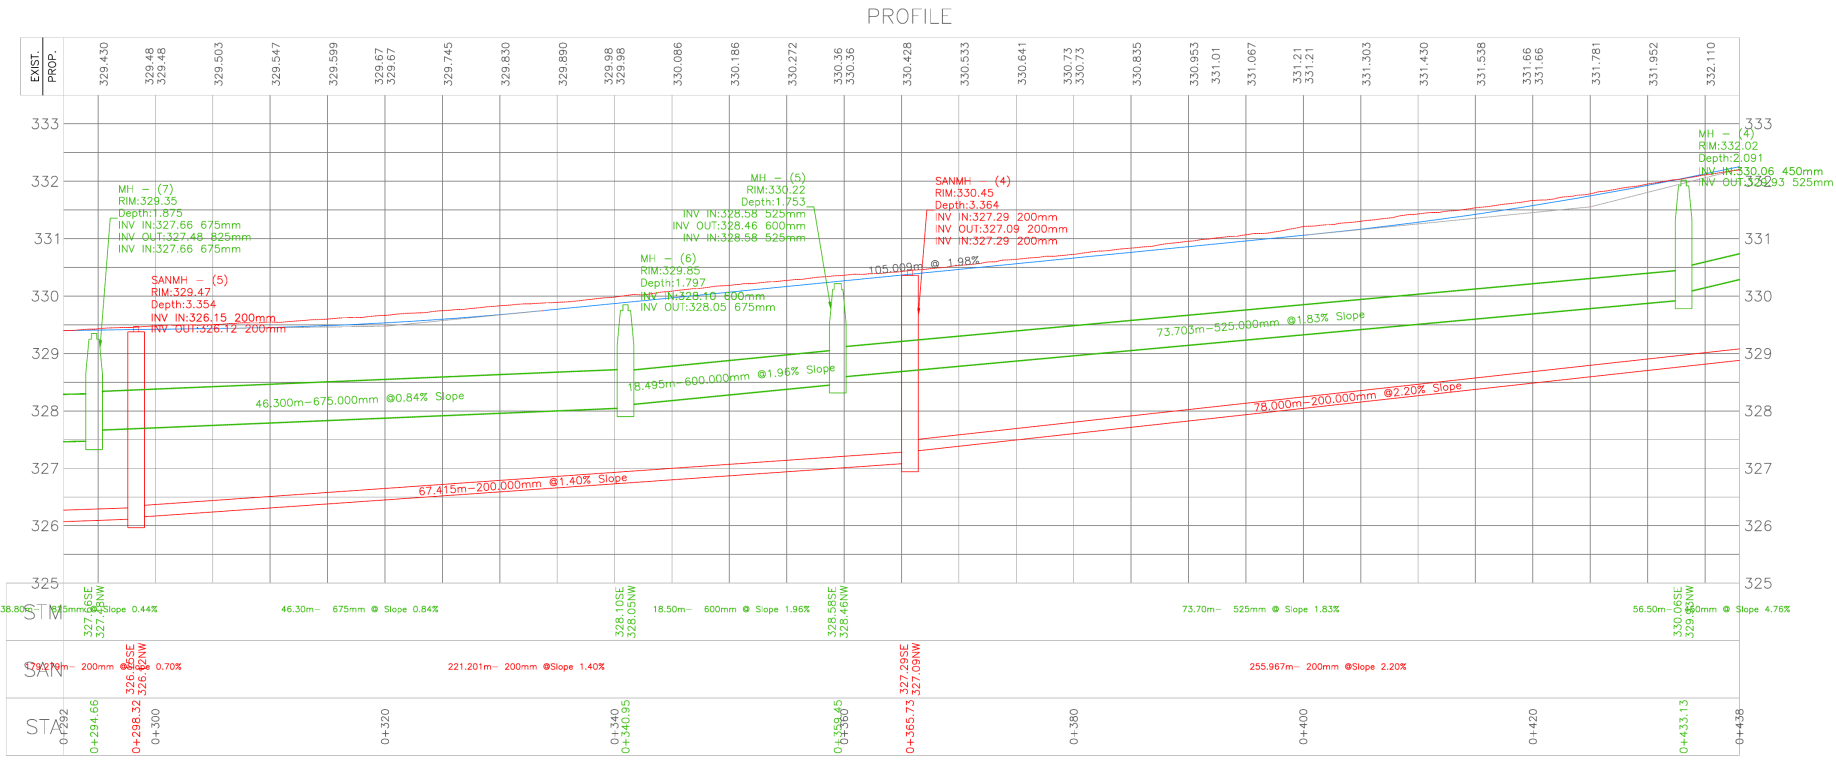
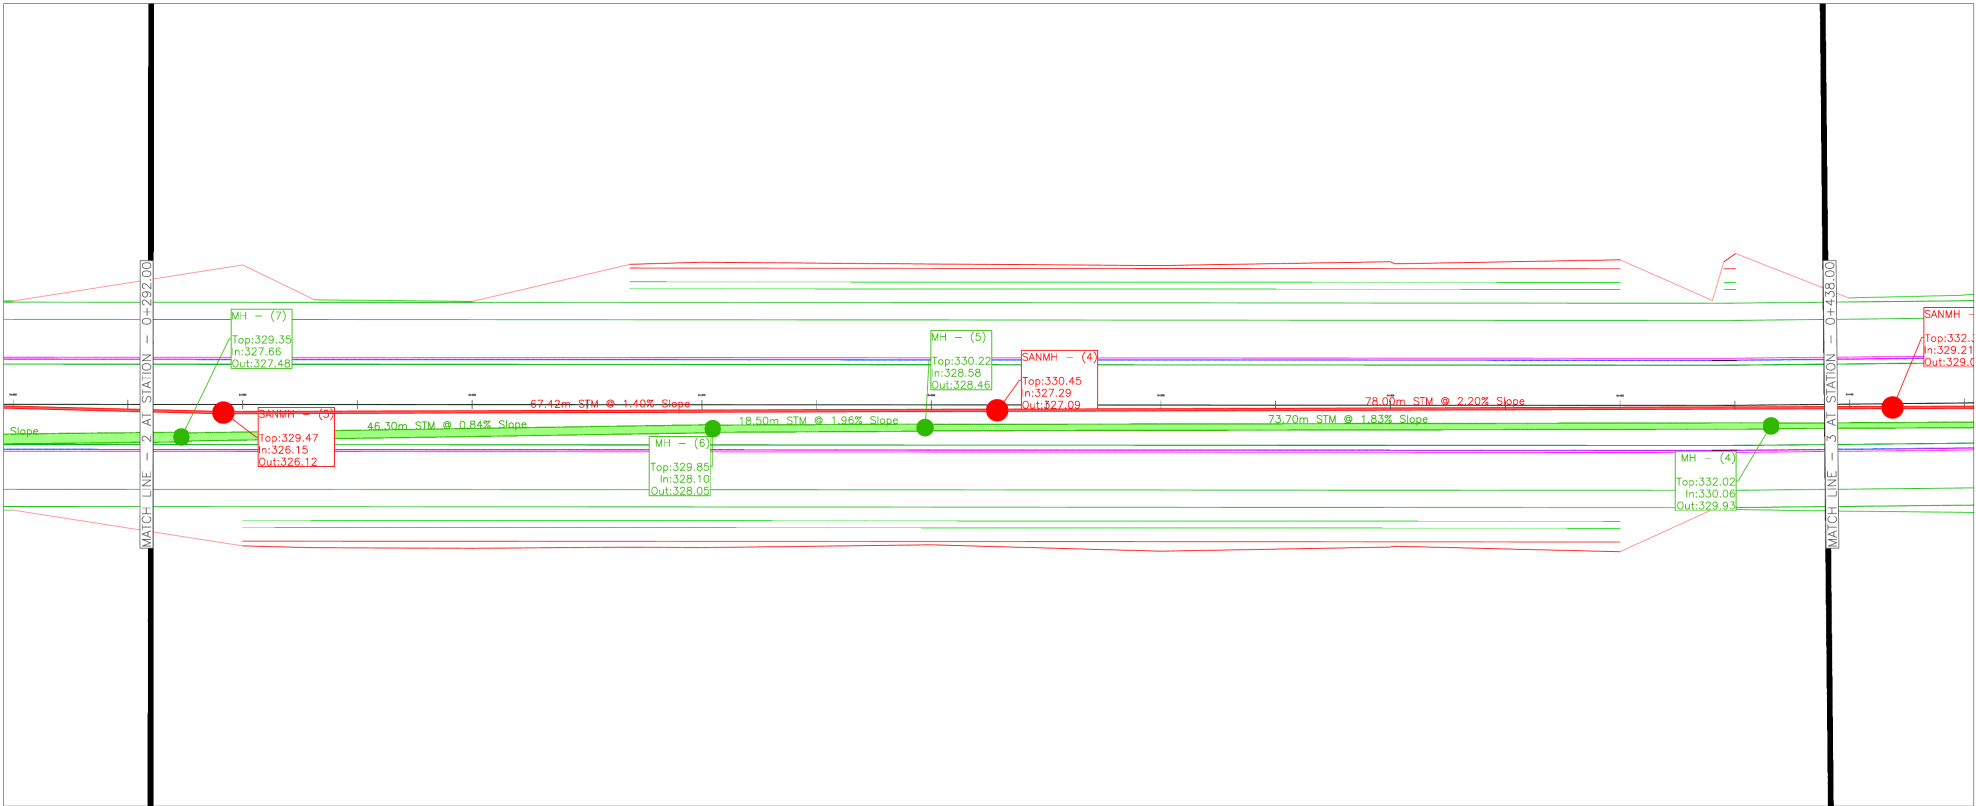


INIT	DATE	REVISIONS

CONSULTANT NAME

Title
Sheet

DATE: August 28, 2026	DESIGN BY: AP
Scale:	DRWAN BY: AP
	CHECKED BY:
	Sheet Numer:
	SheetNumber

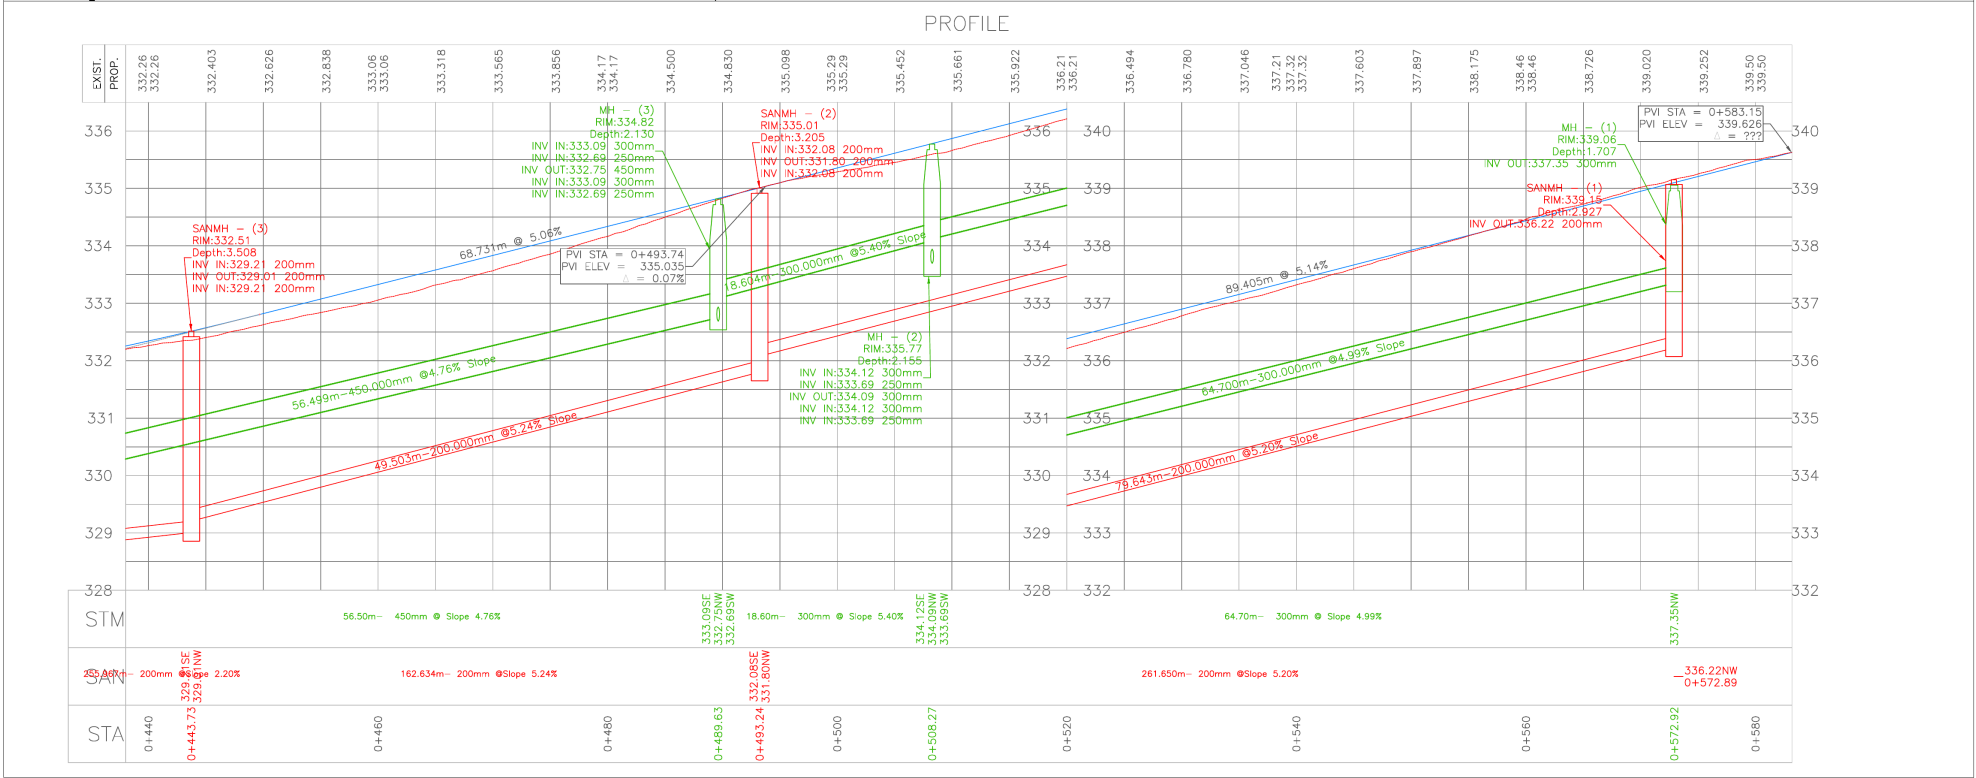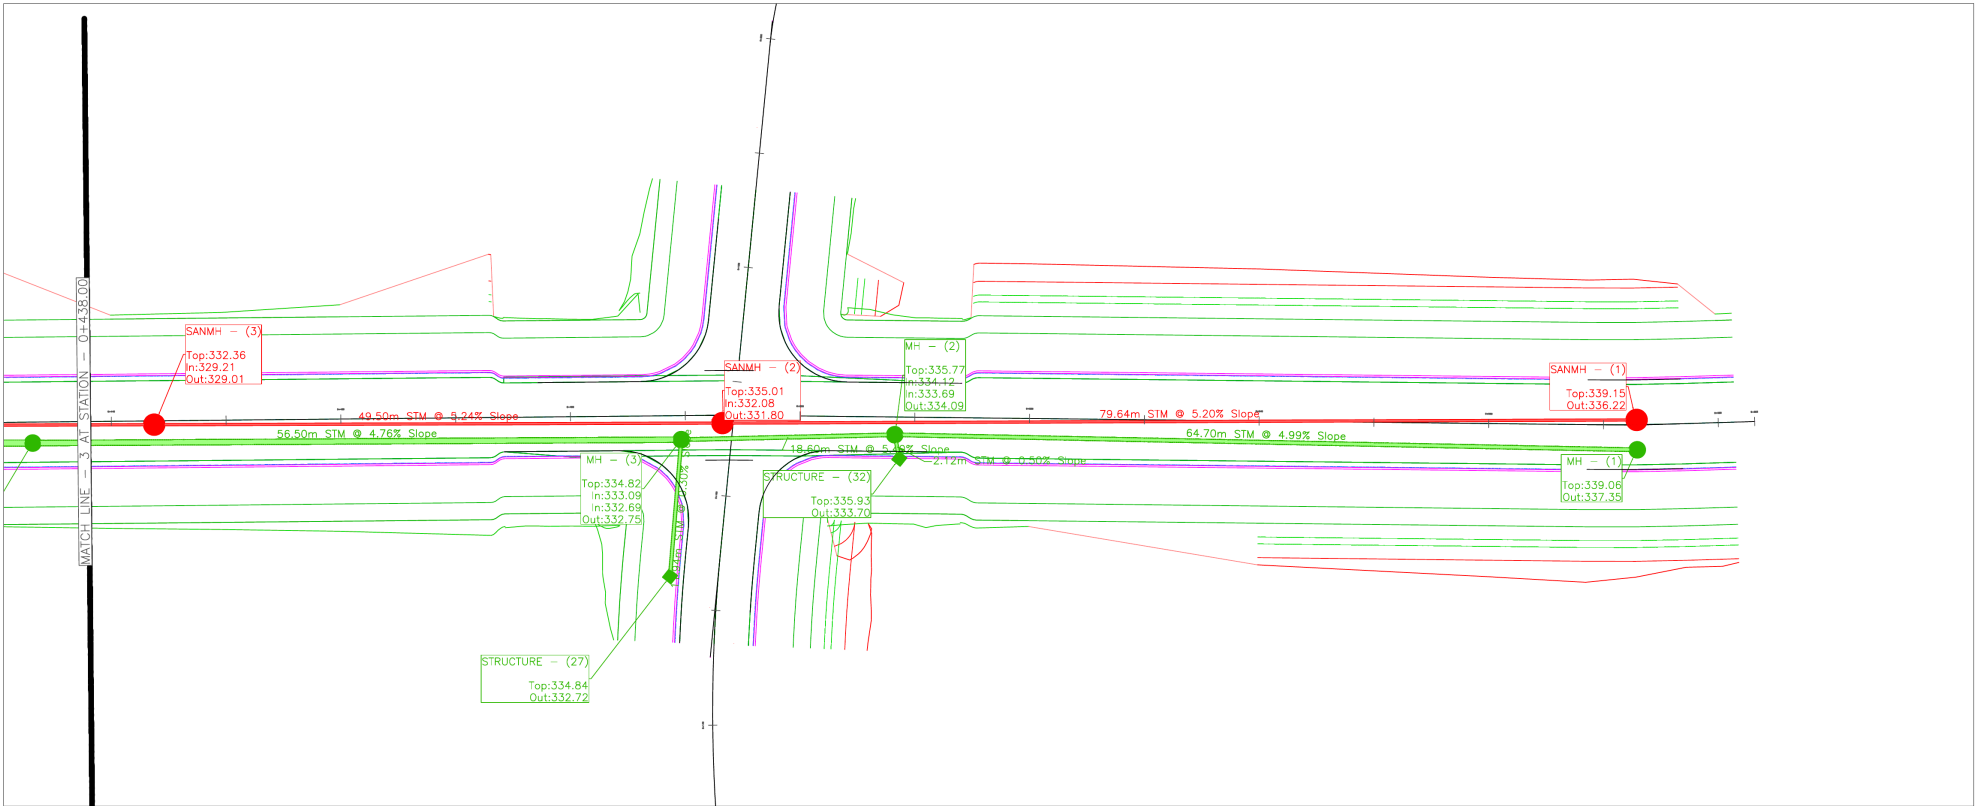

INIT	DATE	REVISIONS

CONSULTANT NAME

Title
Sheet

DATE: August 28, 2026	DESIGN BY: AP
Scale:	DRWAN BY: AP
	CHECKED BY:
	Sheet Numer:
	SheetNumber

Demonstrated Civil 3D capabilities

1

Surface and alignment

Existing-ground organization and alignment-based plan/profile production.

2

Road corridor

Corridor geometry and intersection lane-width transition coordination.

3

Pipe networks

Storm and sanitary pipes, structures, profiles, styles and annotation.

4

Sheet production

View frames, match lines, data bands and colour sheet-set publishing.

PROFESSIONAL USE LIMITATION

This is a skills demonstration—not an issued design, tender document, permit submission, record drawing or construction document. It has not been independently reviewed or sealed.