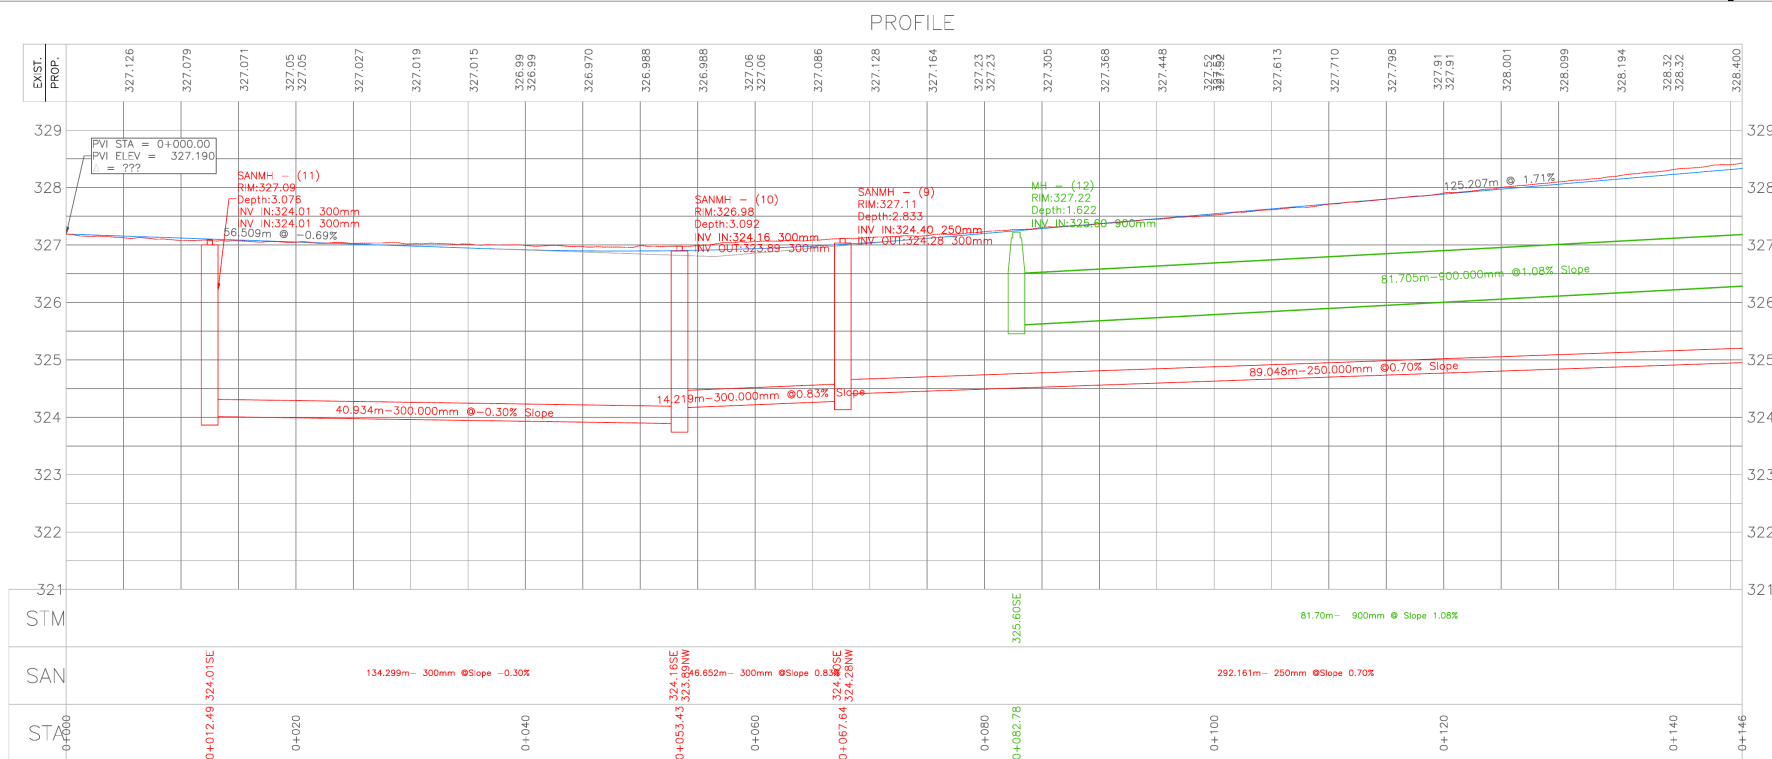




CORE CAPABILITIES

-

This independent conceptual exercise demonstrates a coordinated municipal road, storm sewer and sanitary sewer drawing package. The focus is Civil 3D modelling, plan/profile coordination and drawing production—not construction authorization or final engineering certification.

MODEL DEVELOPMENT	DRAWING PRODUCTION	QUALITY REVIEW
- Existing-ground surface - Road alignment and profile - Corridor and intersection tie-ins - Storm and sanitary networks	- Plan and profile views - Pipe and structure annotation - Profile data bands - View frames and match lines	- Network/profile consistency - Pipe slopes and inverts - Structure placement - Colour plot readability

SheetNumber

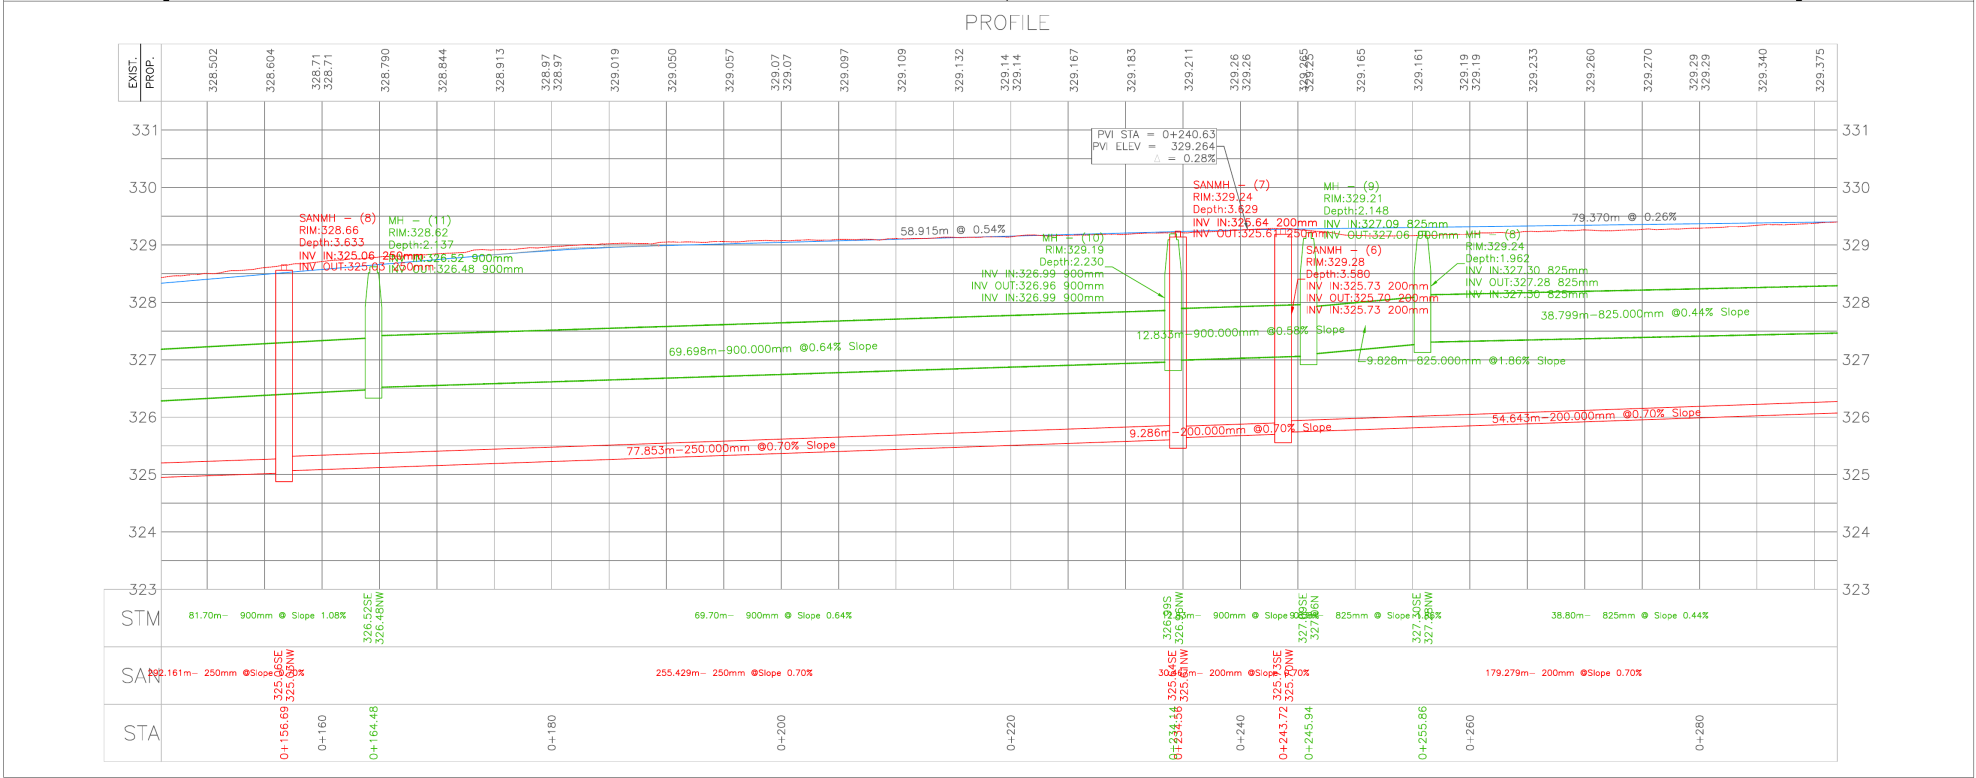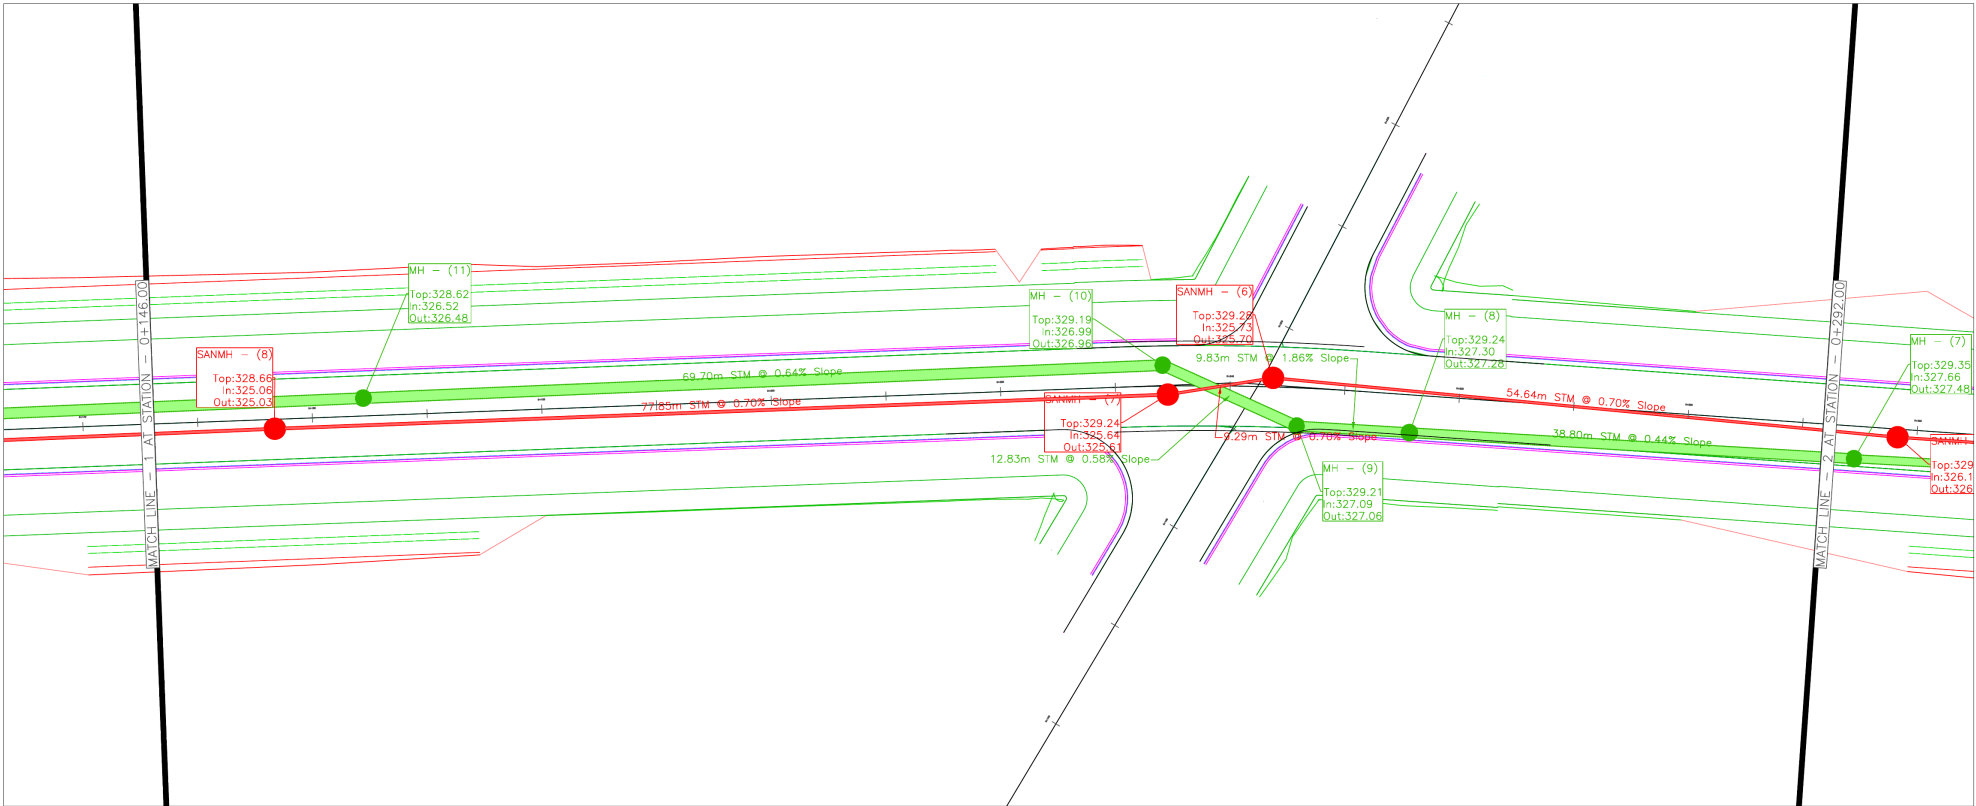



INIT	DATE	REVISIONS

CONSULTANT NAME

Title
Sheet

DATE: August 28, 2026	DESIGN BY: AP
Scale:	DRWAN BY: AP
	CHECKED BY:
	Sheet Numer:
	SheetNumber

Plan and profile sheet 3 of 4

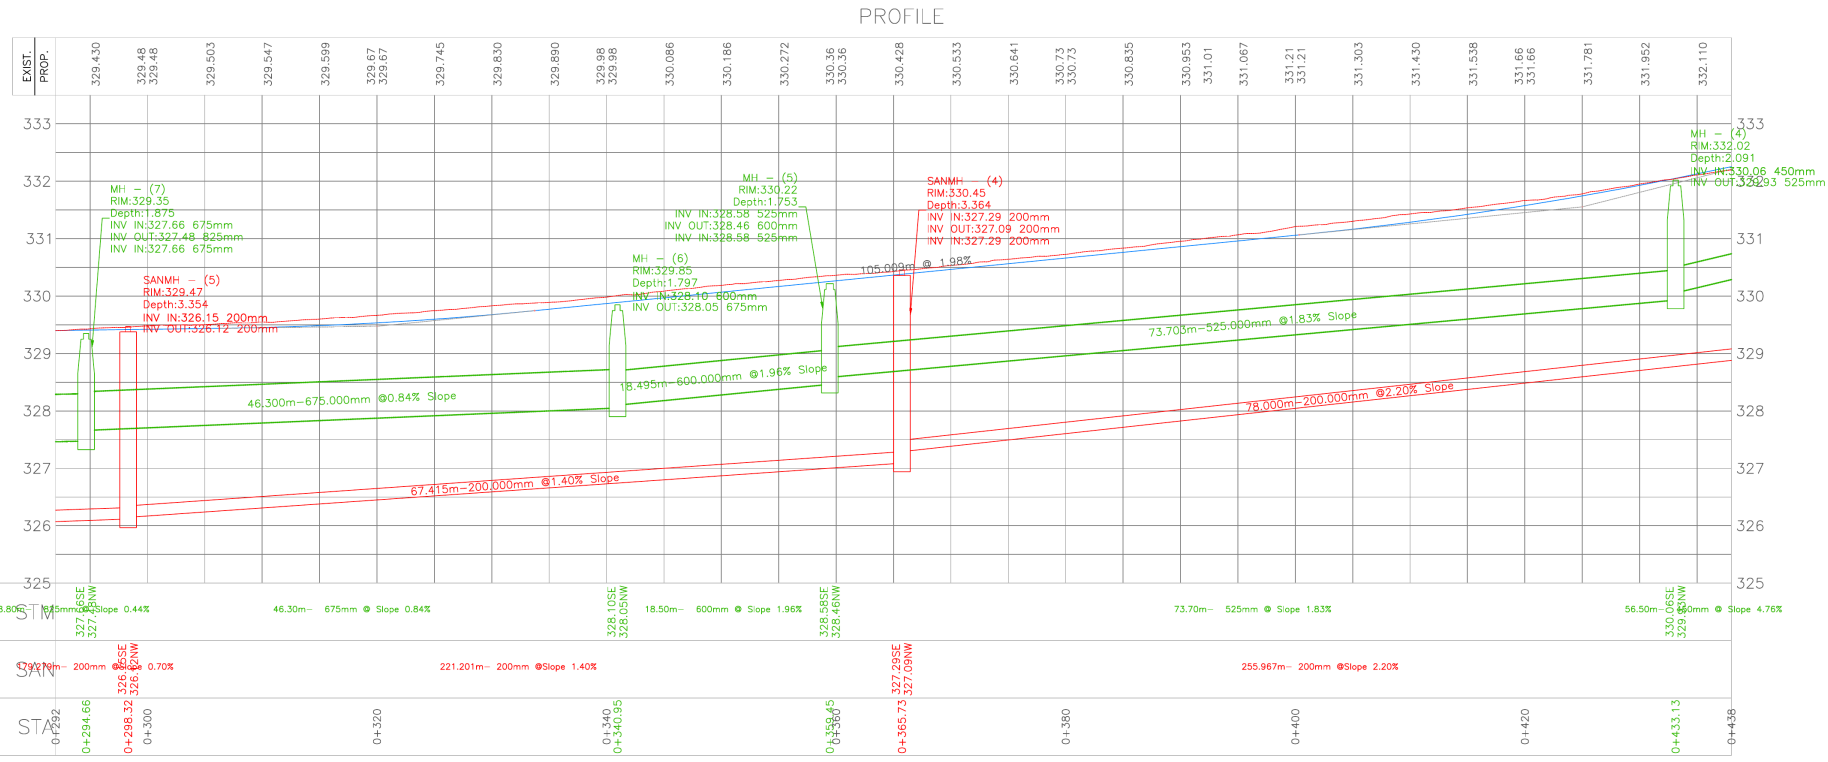
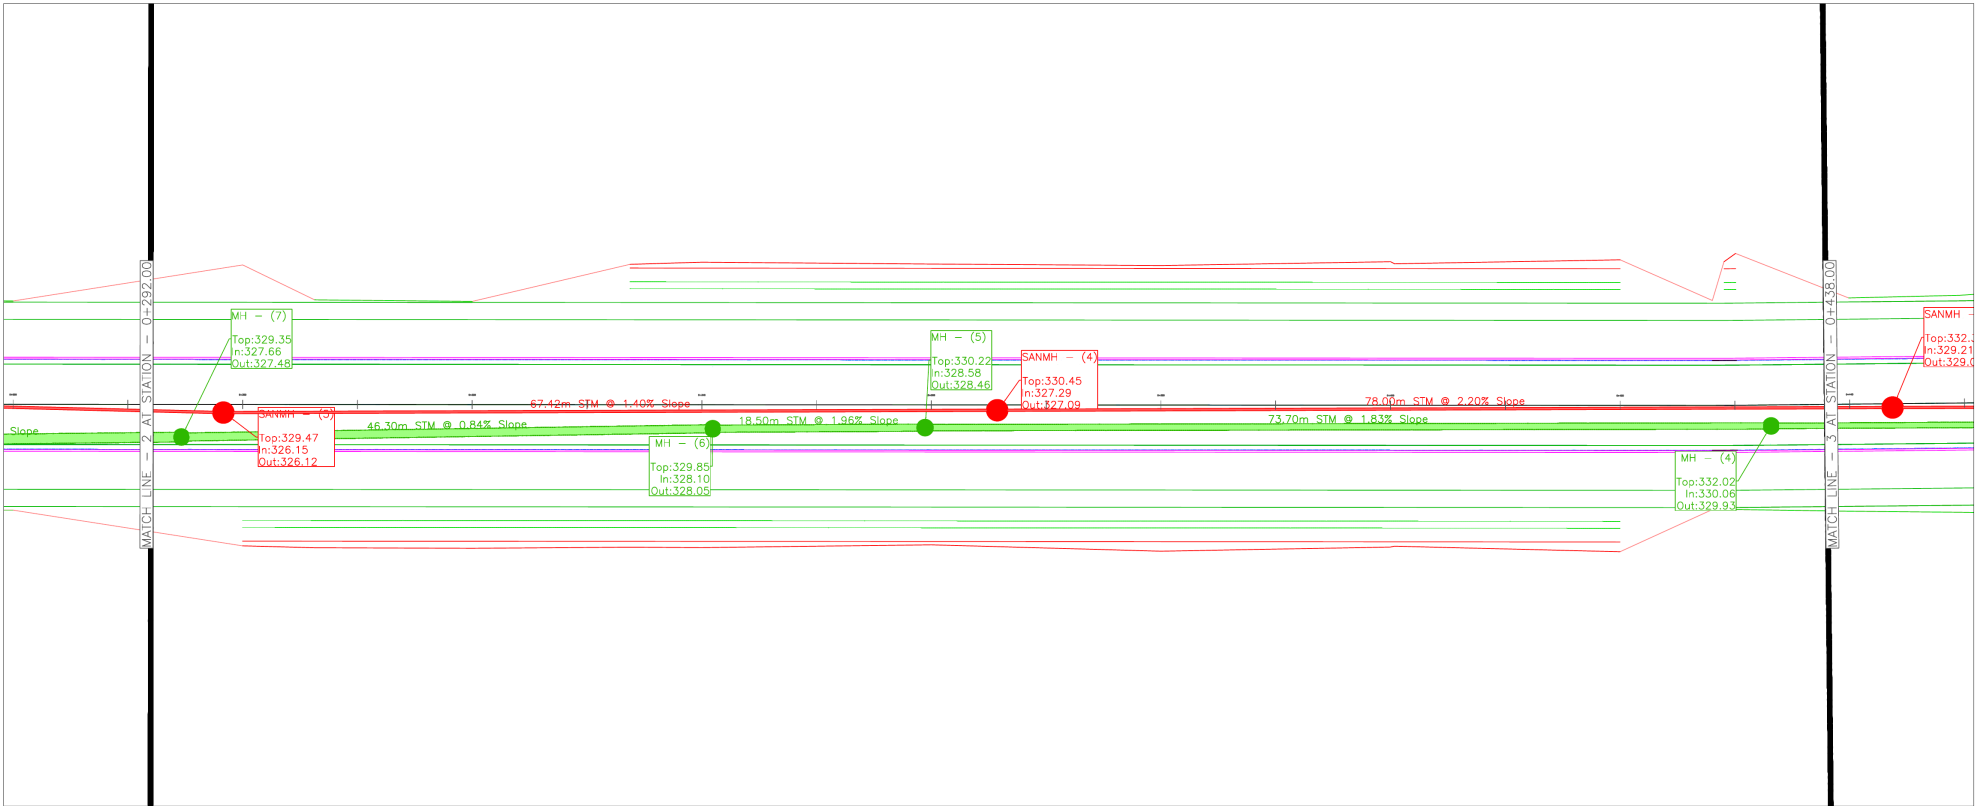


INIT	DATE	REVISIONS

CONSULTANT NAME

Title
Sheet

DATE: August 28, 2026	DESIGN BY: AP
Scale:	DRWAN BY: AP
	CHECKED BY:
	Sheet Numer:
	SheetNumber

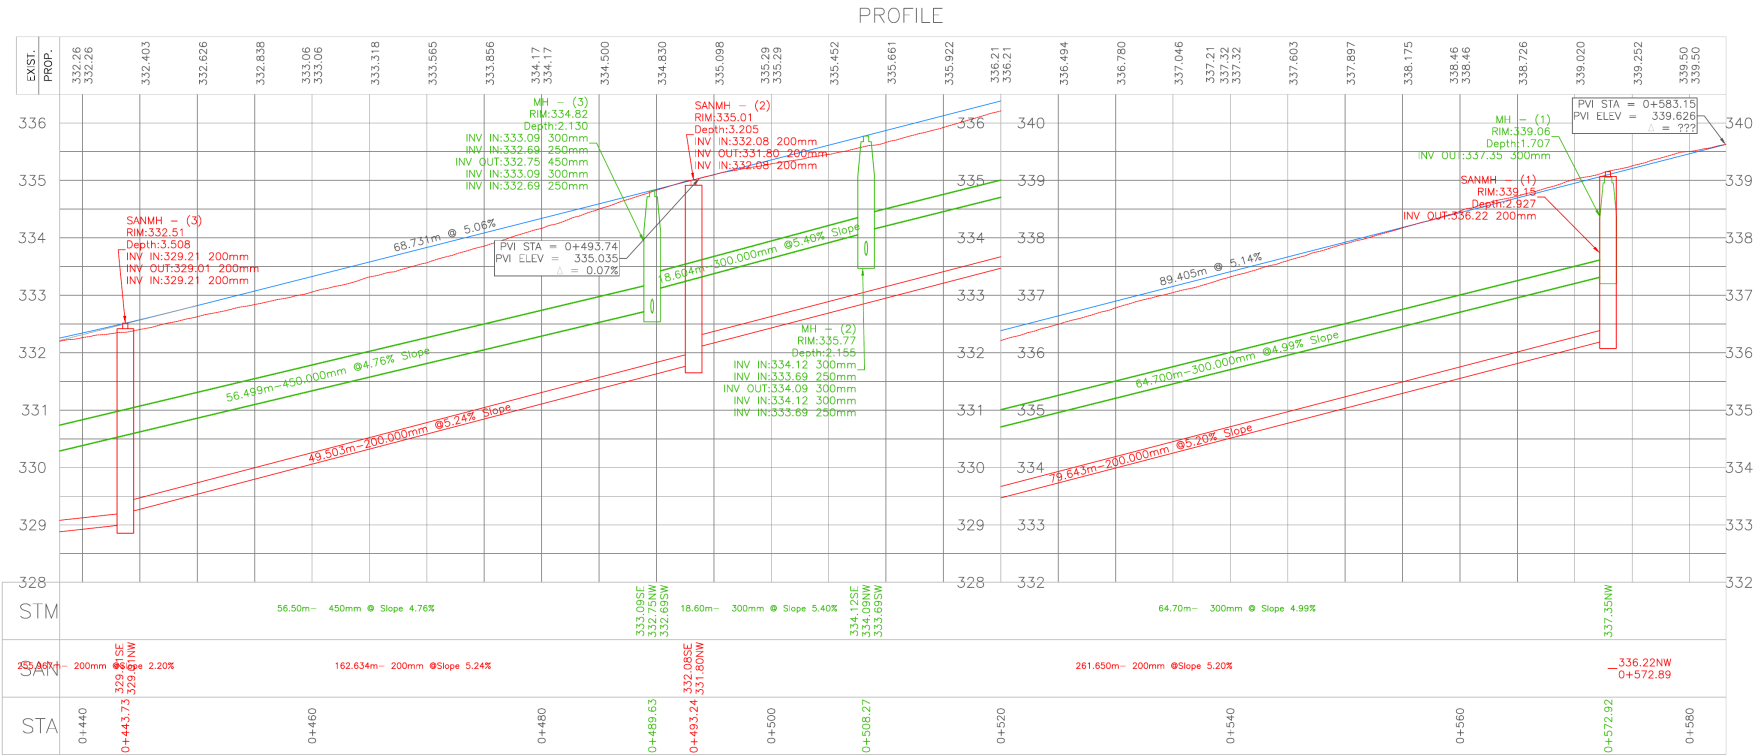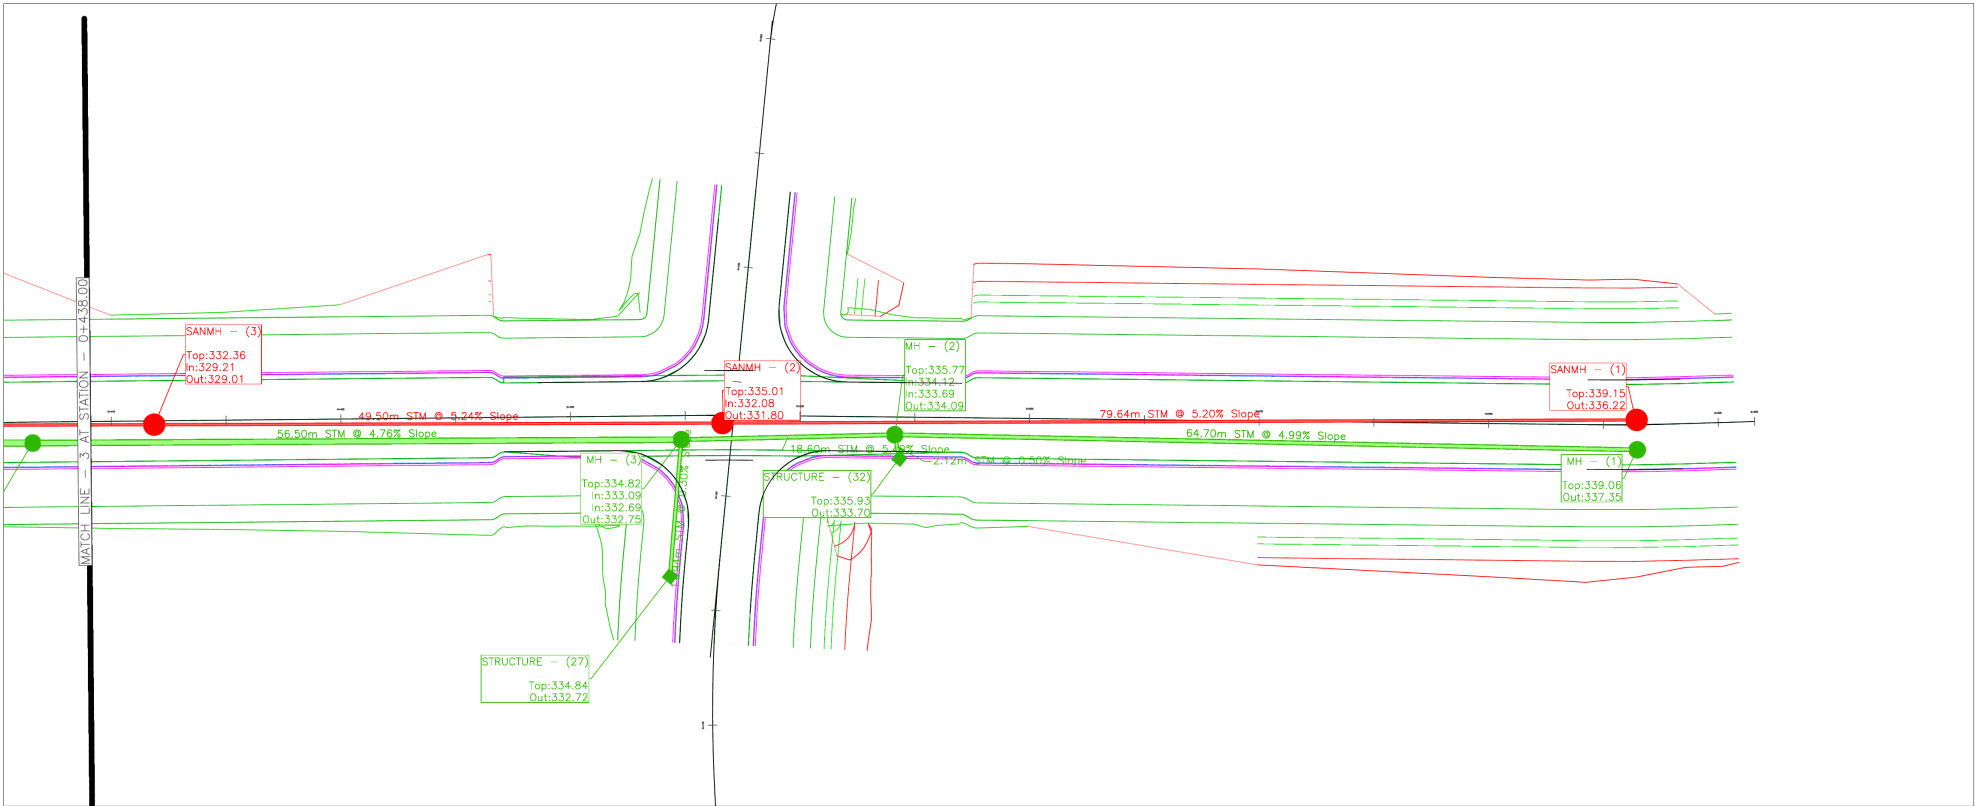

INIT	DATE	REVISIONS

CONSULTANT NAME

Title
Sheet

DATE: August 28, 2026	DESIGN BY: AP
Scale:	DRWAN BY: AP
	CHECKED BY:
	Sheet Numer:
	SheetNumber

Demonstrated Civil 3D capabilities

1

Surface and alignment

Existing-ground organization and alignment-based plan/profile production.

2

Road corridor

Corridor geometry and intersection lane-width transition coordination.

3

Pipe networks

Storm and sanitary pipes, structures, profiles, styles and annotation.

4

Sheet production

View frames, match lines, data bands and colour sheet-set publishing.

PROFESSIONAL USE LIMITATION

This is a skills demonstration—not an issued design, tender document, permit submission, record drawing or construction document. It has not been independently reviewed or sealed.